
PRODUCED BY AN AUTODESK EDUCATIONAL PRODUCT

PRODUCED BY AN AUTODESK EDUCATIONAL PRODUCT

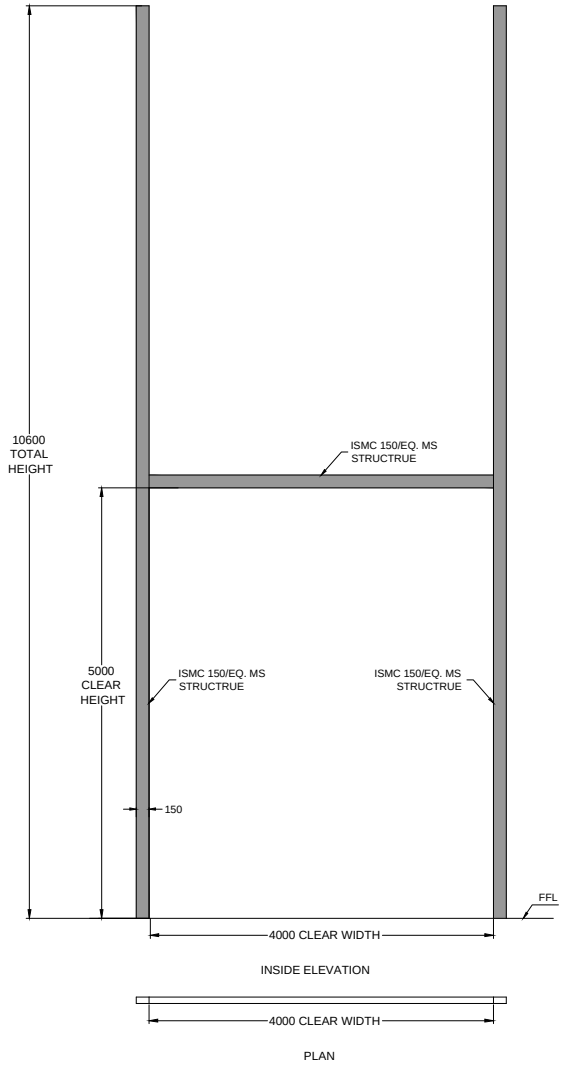

DIMENSION :

CLEAR WIDTH	CLEAR HEIGHT	QUANTITY
4000 mm	5000 mm	01

IMPORTANT NOTES:
1. REQUIRED STRUCTURE FOR DOOR SHALL BE IN CLIENT'S SCOPE.
2.SINGLE PHASE POWER SUPPLY REQUIRED AT DOOR LOCATION.
3.ALL CIVIL WORK SHALL BE CLIENT'S SCOPE.

NIHVA
NIHVA TECHNOLOGIES PVT. LTD.
NIHVA TECHNOLOGIES PVT. LTD. PUNE
Email:- info@nihva.com
Website:- www.nihva.com

TITLE:

STRUCTURE FOR
SECTIONAL DOOR VL (MOTORIZED)

CLIENT'S APPROVAL :

CLIENT -LM WIND POWER

PROJECT -

SITE LOCATION - GUJARAT

DWG. NO. : NIHVA/17-18/0396 | REV- 1

SCALE: NTS | WT: | SHEET:1 OF 1

	NAME	DATE	SIGN
DRAWN	OMKAR	09-03-2018	
CHECK	SHEKHAR	09-03-2018	
APPROVAL	SHEKHAR	09-03-2018	

If any queries contact : design@nihva.com

NOTE: ALL DIMENSIONS ARE IN mm

THIS DRAWING & DESIGNING IS THE PROPERTY OF NIHVA TECHNOLOGIES. NOT TO BE SOLD OR COPIED TO ANY OTHER CONCERN.

PRODUCED BY AN AUTODESK EDUCATIONAL PRODUCT

PRODUCED BY AN AUTODESK EDUCATIONAL PRODUCT