




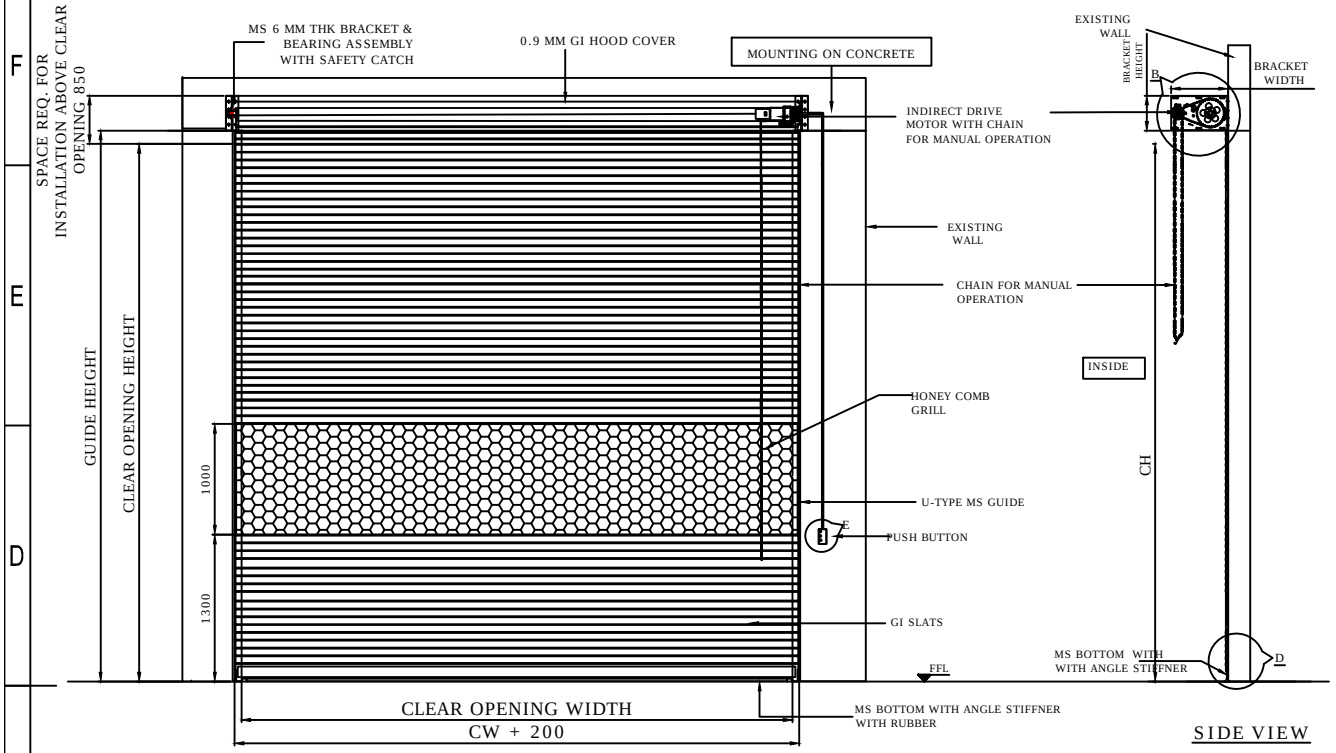


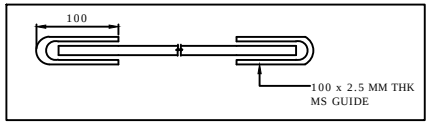

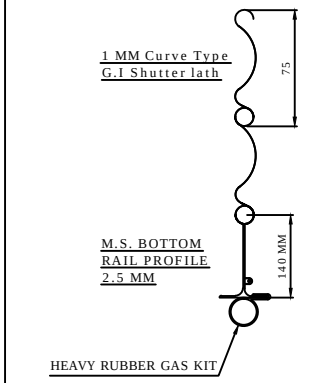

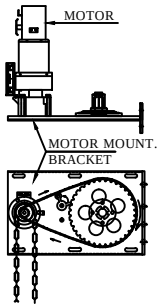

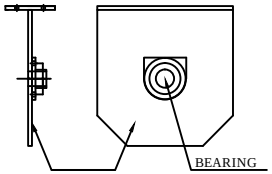

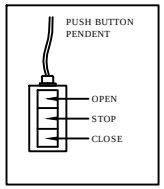

RAL CODE	SHADE	COLOUR
RAL 7037	DUSTY GREY	

SR NO	CLEAR OPENING WIDTH(CW)	CLEAR OPENING HEIGHT(CH)	QTY	LOCATION	MOTOR SIDE (RH/LH SEEN FROM INSIDE)	MOUNTING INsIDE/OUTSIDE
6	5310	4020	1	DG1	RH	INSIDE
5	4690	4025	1	DG2	RH	INSIDE
4	2510	3050	1	PUMP ROOM	RH	INSIDE
3	2510	3050	1	BOILER 3	RH	INSIDE
2	3990	3260	1	BOILER 1	RH	INSIDE
1	3990	3260	1	BOILER 2	RH	INSIDE

NOTES-
(1) THIS DRAWING IS FOR MOUNTING OF ROLLING SHUTTERS ON CONCRETE.
(2) ALL CIVIL WORK AT SITE IS IN CLIENT SCOPE.

This drawing & design is the property of NIHVA TECHNOLOGIES. Not to be sold or copied to any other concern.

TITLE- GI SLAT MOTORIZED ROLLING SHUTTER

NIHVA TECHNOLOGIES PVT. LTD.

NIHVA TECHNOLOGIES PVT. LTD. PUNE
Tel : 020 66304033
Email:- info@nihva.com
Website:- www.nihva.com

	NAME	SIGN	DATE
DRAWN	SIDDHESHWAR		7.1.2021
CHECK	SIDDHESHWAR		7.1.2021
APPRD.			

CLIENT -
PROJECT -
SITE LOCATION -

If any queries contact : projectsupport@nihva.com

DWG. NO. : NIHVA/20-21/VDR/0101 REV- R00

ALL DIMENSION ARE IN mm

SCALE: NTS WT: SHEET: