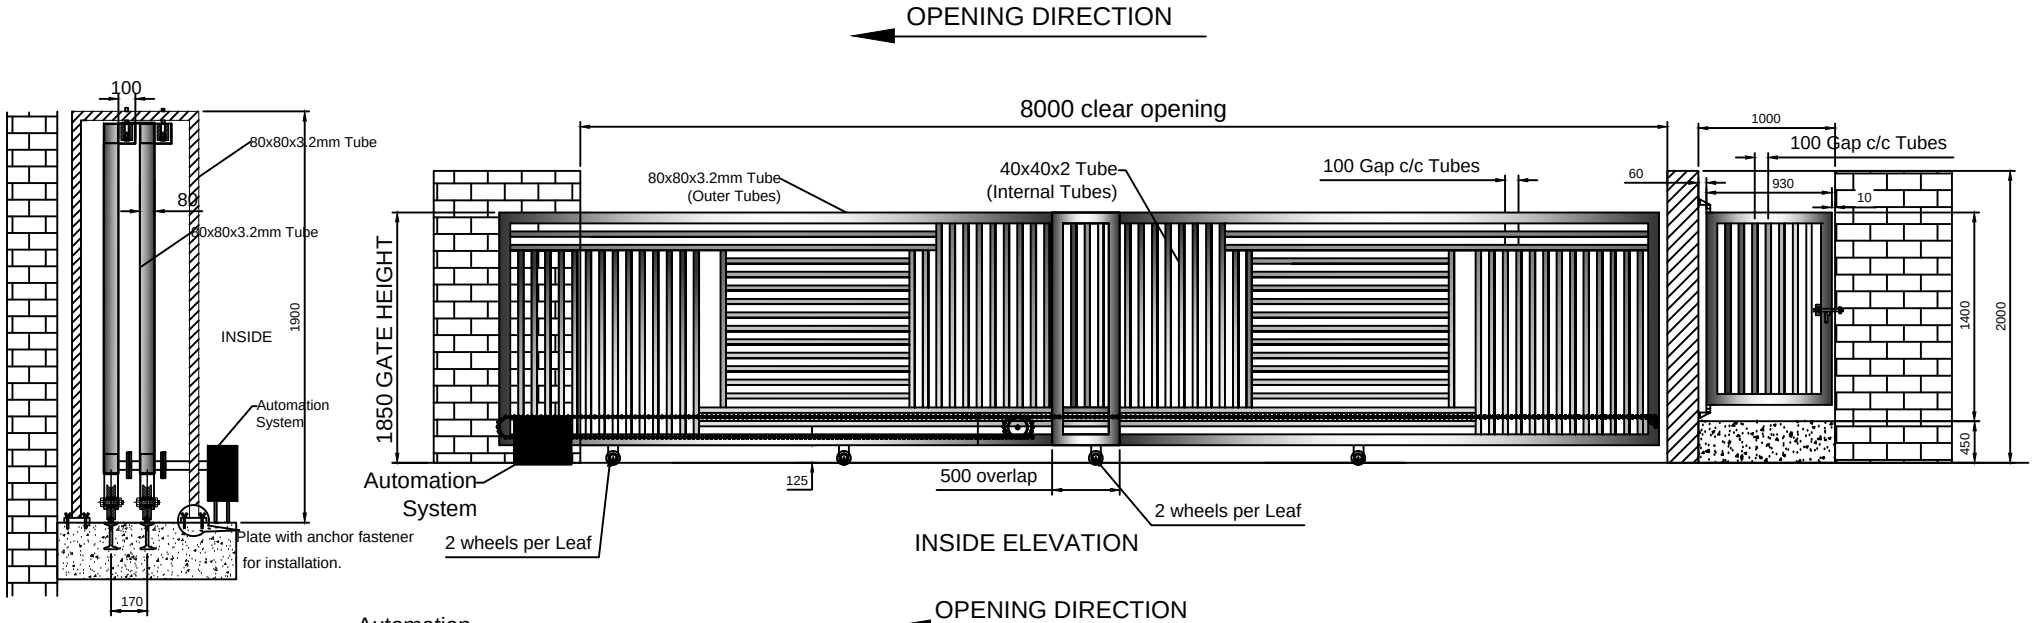


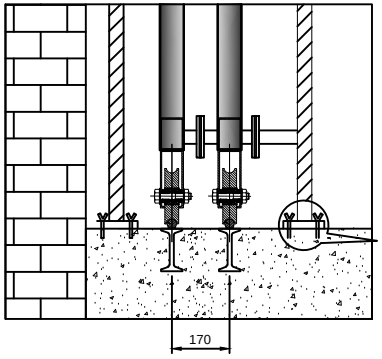


Plate with anchor fastener for installation.

Clear Opening size -8000mm x 1850mm
& Wicket gate opening size-1000x1400mm

NOTE :- *ALL REQ. CIVIL WORK WILL BE IN CLIENT SCOPE.

DOUBLE LEAF TELESCOPIC GATE & WICKET GATE

This drawing & designing is the property of NIHVA TECHNOLOGIES. Not be sold or copy to any other concern.

TITLE		
DOUBLE LEAF TELESCOPIC SLIDING GATE& WICKET GATE		
	SIGN	DATE
DRAWN	OMKAR	25/02/16
CHECK	ANIL	25/02/16
REV.	01	
APPROVAL		

NIHVA TECHNOLOGIES PVT. LTD.
NIHVA TECHNOLOGY PVT. LTD. PUNE
Tel : 020 66304033
Email:- info@nihva.com
Website:- www.nihva.com

CLIENT -
PROJECT -
SITE -
DWG. NO. : NIHVA/15-16/

If any queries contact : projects@nihva.com | SCALE: 01 | WT: | SHEET: 01 OF 01

ALL DIMENSION ARE IN mm