

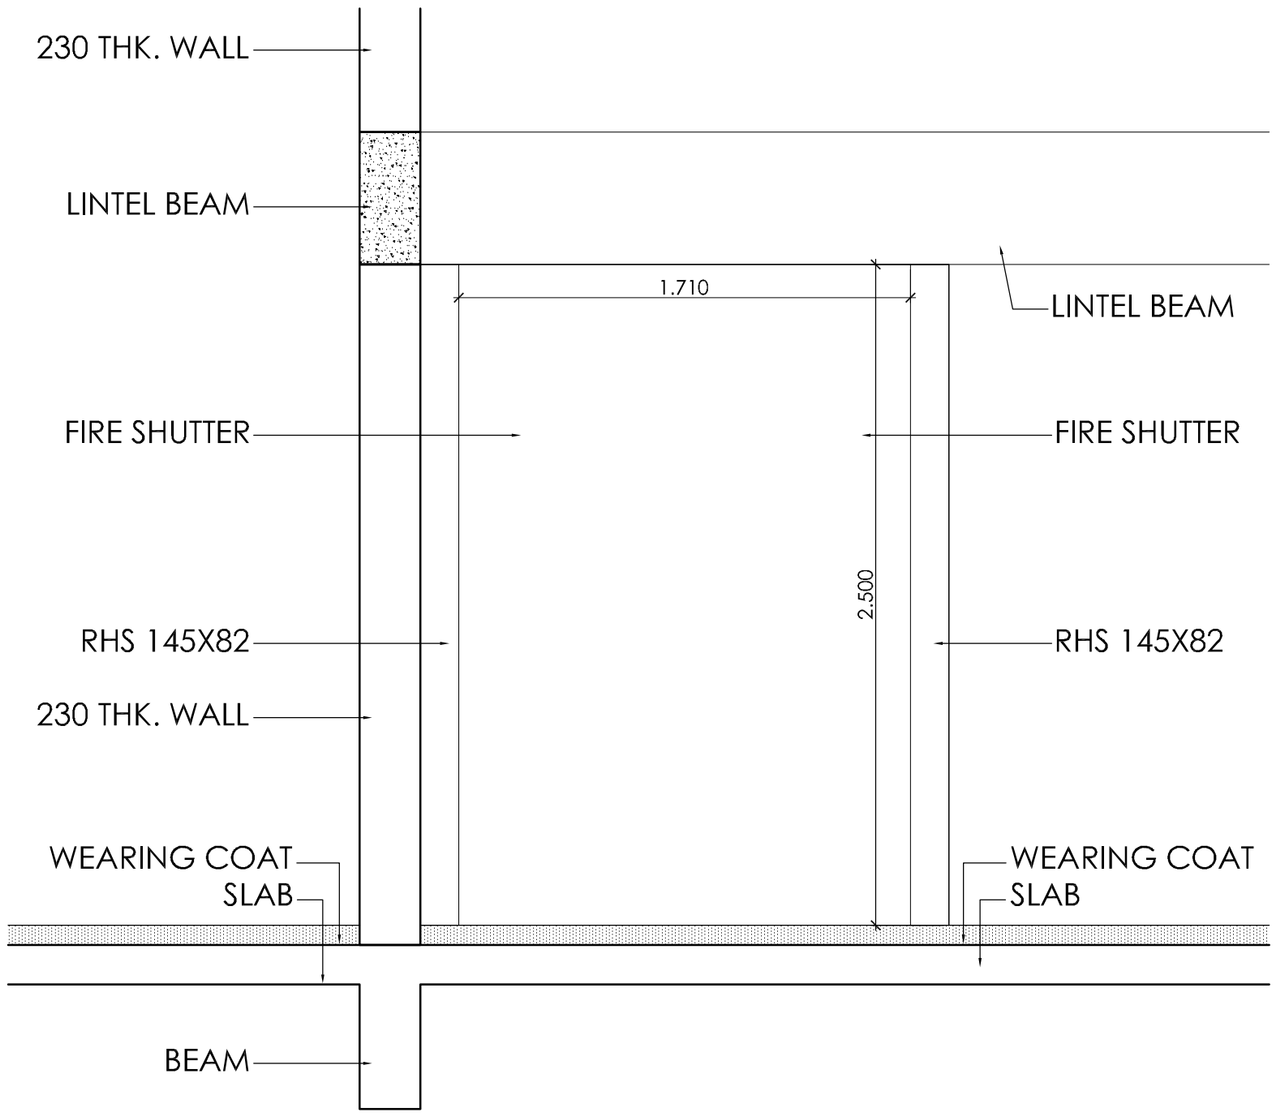



FIRE SHUTTER FARMING ELEVATION

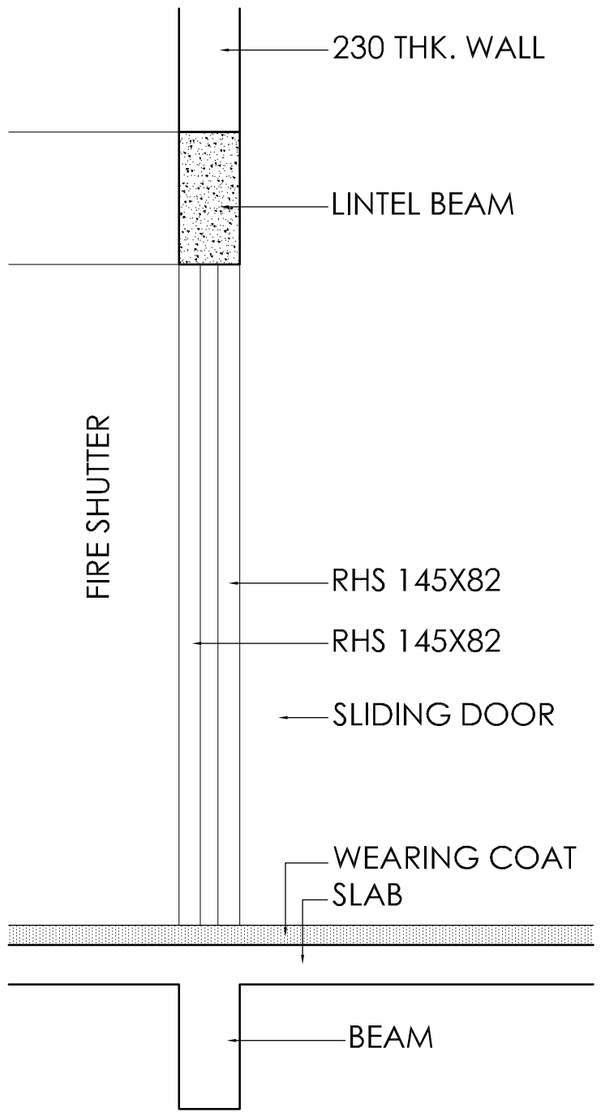

CROSS SECTION

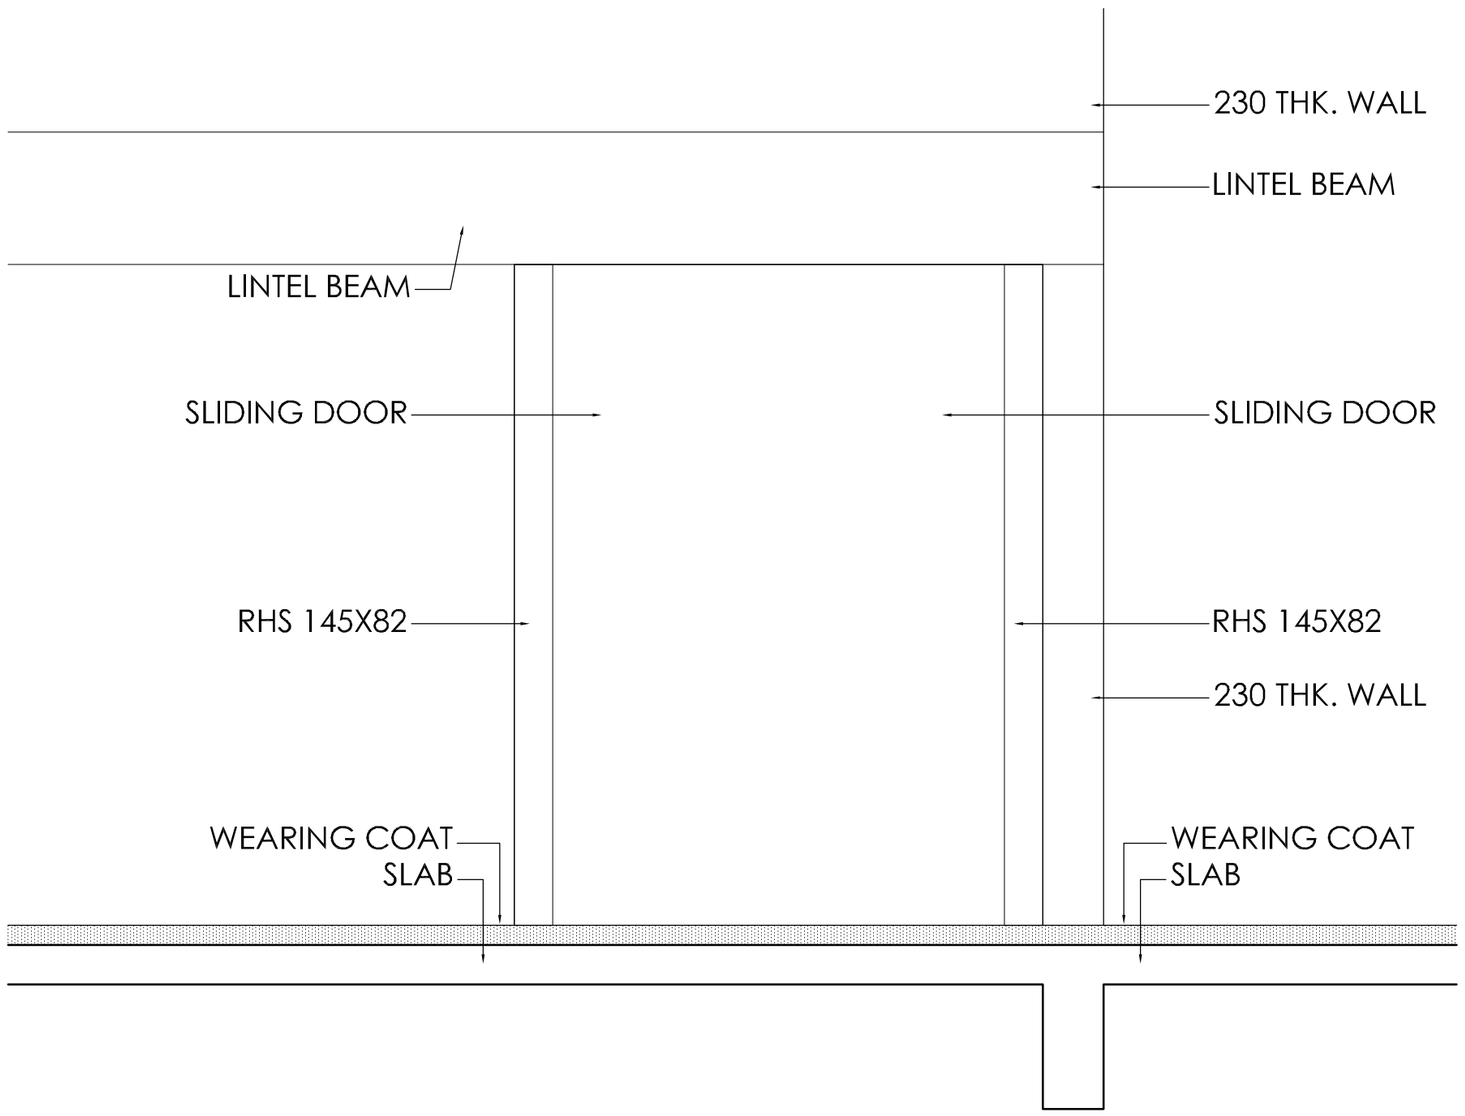

SLIDING DOOR FARMING ELEVATION

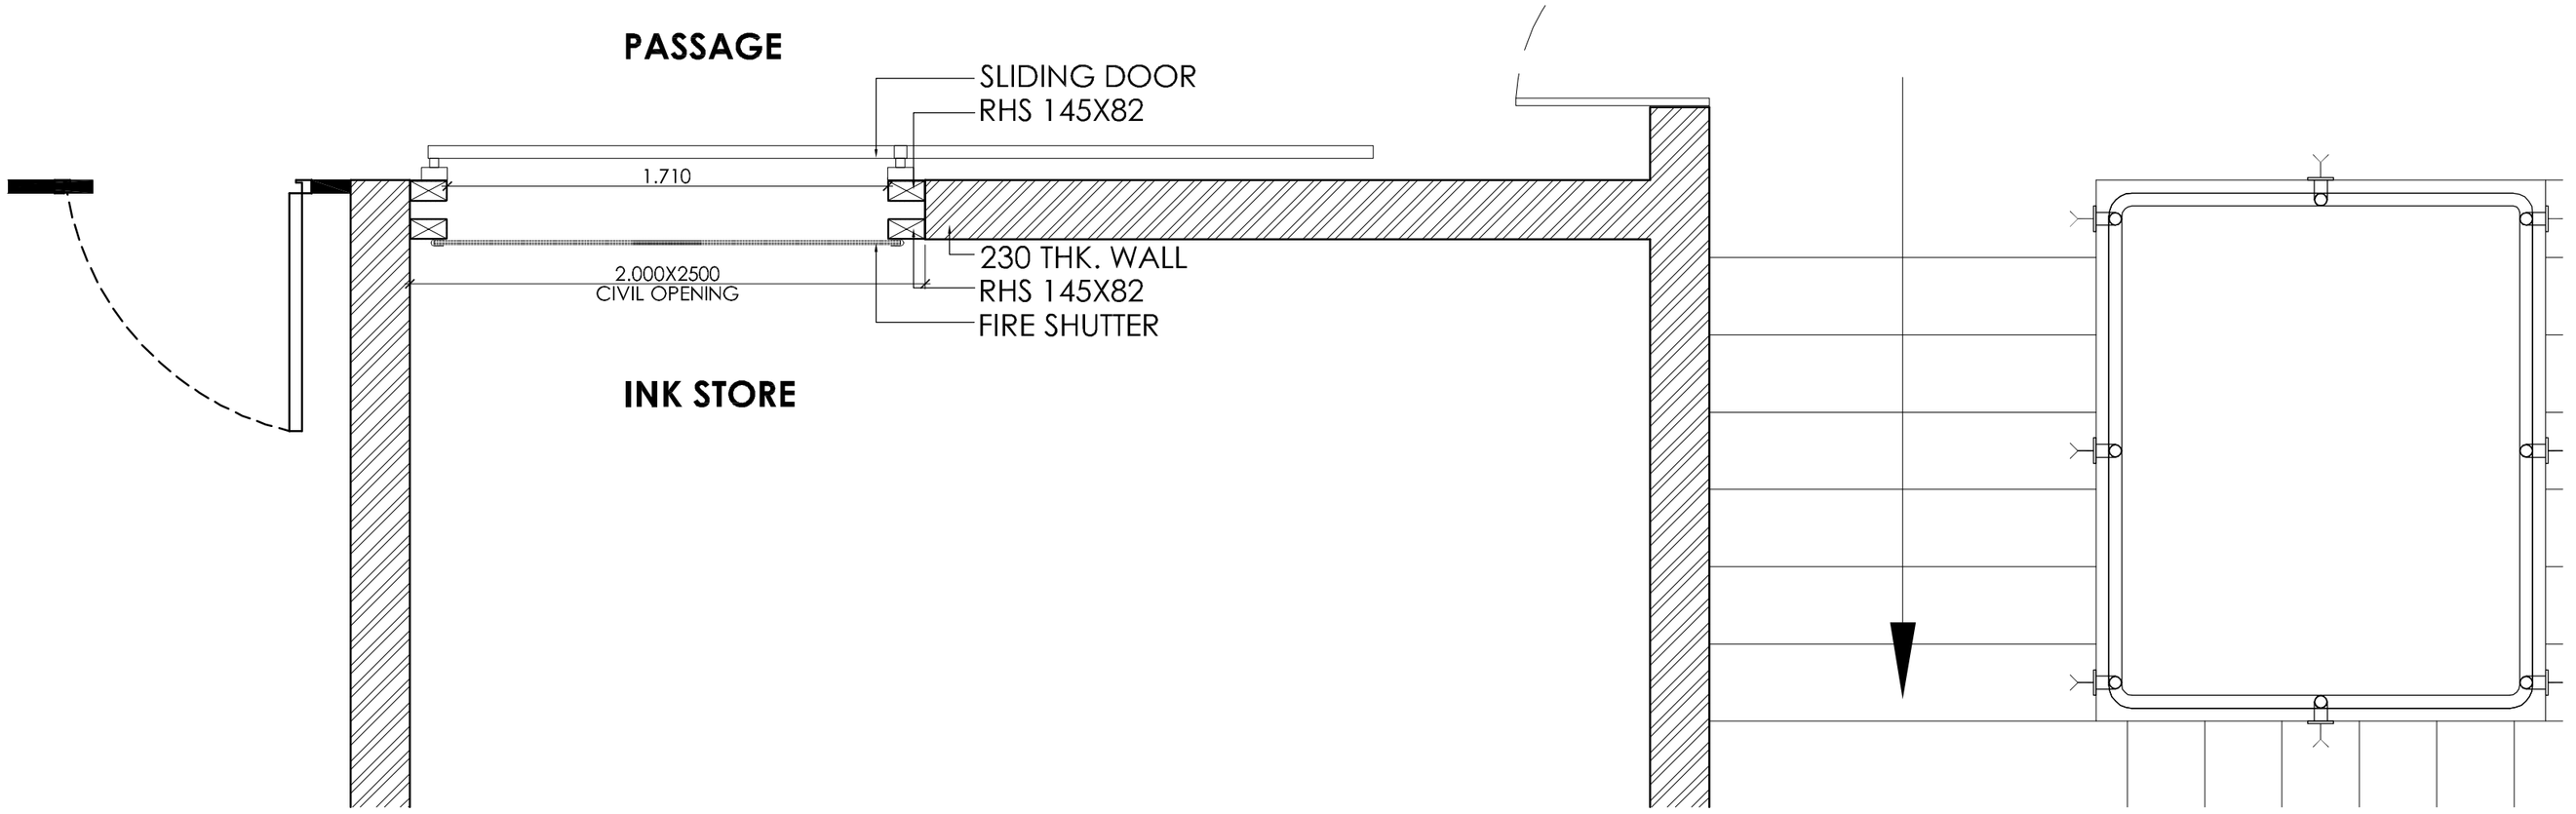

SLIDING DOOR & FIRE SHUTTER FARMING PLAN

R. NO.	DATE	REVISION

REVISION

PROJECT

PROPOSED PLANT AT PLOT NO. B-38/1,
CHAKAN INDUSTRIAL AREA, PH-II,
VASULI, KHED, PUNE.
FOR PACK TIME INNOVATIONS PVT LTD.

TITLE

FIRST FLOOR INK STORE ROOM
DOOR FARMING DETAILS

G.A. DRAWING :- ☐	REFERENCE DRG :- ☐
APPROVAL DRG :- ☑	GFC. DRAWING :- ☐

DATE	SCALE	DRG. NO	JOB. NO	NORTH
04.10.2017	1 : 30	INK STORE - 02	PTI-1508	
	Drn :Motiram	Chd :RSS		

Dandekar and Associates
ARCHITECTS - ENGINEERS
FLAT NO 4, AVIVA APT. LANE NO. 3 PRABHAT RD, ERANDWANA
PUNE-411004.PH.25667050/4358 Email- dandekar.pti@gmail.com

\\Main-pc\ad\AD\PTI\DRAWING\WD\3001.dwg Nihva Door