



PRODUCED BY AN AUTODESK EDUCATIONAL PRODUCT

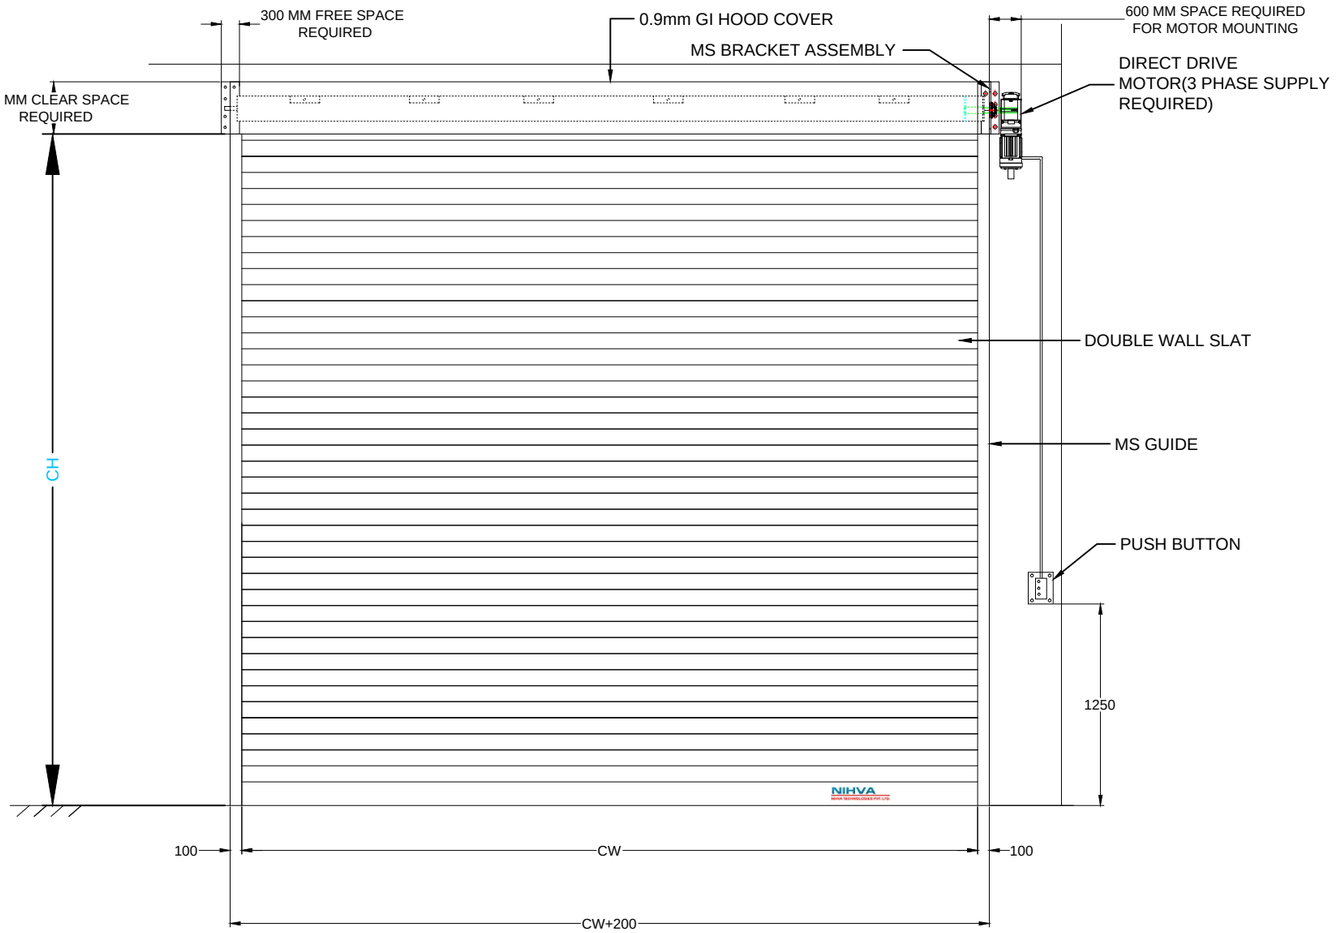

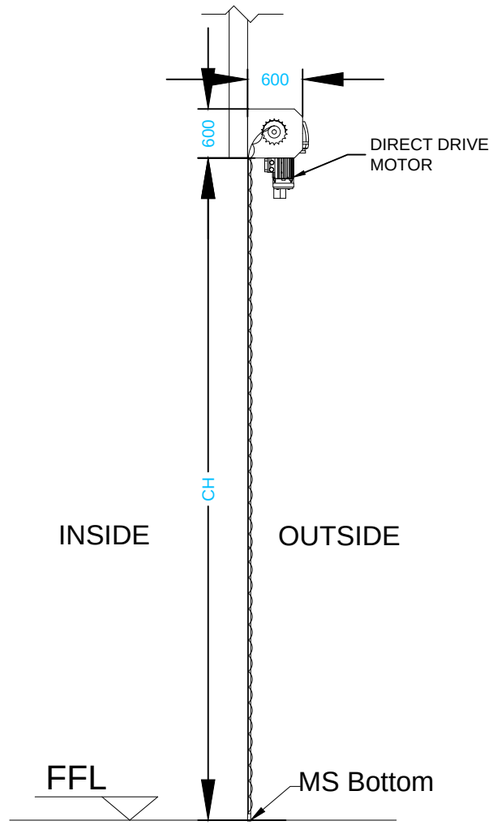

Section A-A

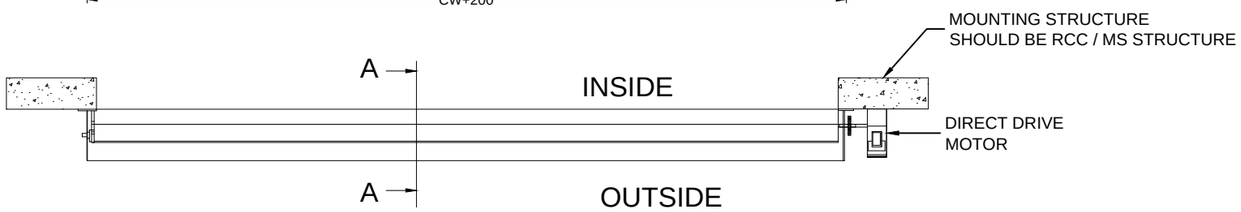


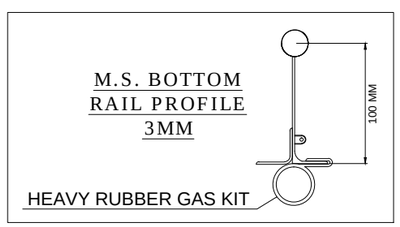

COLOR OF SLATS & SHUTTER -RAL9002 (GRAY WHITE)

Rev.no	Revision	Revised BY	Date
1.	Mentioned title name RS03	Sujata	28/12/2021
2.	Mentioned puff rolling shutter	Sujata	28/12/2021
3.	Changed view of the rolling shutter	Sujata	28/12/2021
4.	Mentioned inside and outside in side view	Ganesh	29/12/2021

Main Slats
Double Wall Puff Rolling Shutter

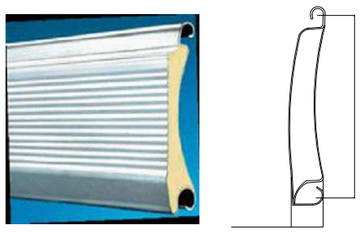

DIMENSION :

CLEAR WIDTH	CLEAR HEIGHT	QUANTITY
3600 mm	3800 mm	1 NOS

NOTE:-

1. 3 PHASE SUPPLY SHOULD BE PROVIDED.

NIHVA TECHNOLOGIES PVT. LTD.
NIHVA TECHNOLOGIES PVT. LTD. PUNE
Email:- info@nihva.com
Website:- www.nihva.com

TITLE:

DOUBLE WALL ROLLING SHUTTER RS03. LGF East side

CLIENT'S APPROVAL :

CLIENT - AJAY KALE AND ASSOSIATE

PROJECT -

SITE LOCATION - PIRANGUT

DWG. NO. : NIHVA/21-22/CLT/294

SCALE: NTS	WT:	SHEET:01 OF 02

DRAWN BY: G.P.	DATE: 23-12-2021
CHECKED BY: A.K.	DATE: 23-12-2021
APPROVED BY :	

If any queries contact : design@nihva.com

NOTE: ALL DIMENSIONS ARE IN mm

THIS DRAWING & DESIGN IS THE PROPERTY OF NIHVA TECHNOLOGIES. NOT TO BE SOLD OR COPIED TO ANY OTHER CONCERN.

PRODUCED BY AN AUTODESK EDUCATIONAL PRODUCT

PRODUCED BY AN AUTODESK EDUCATIONAL PRODUCT