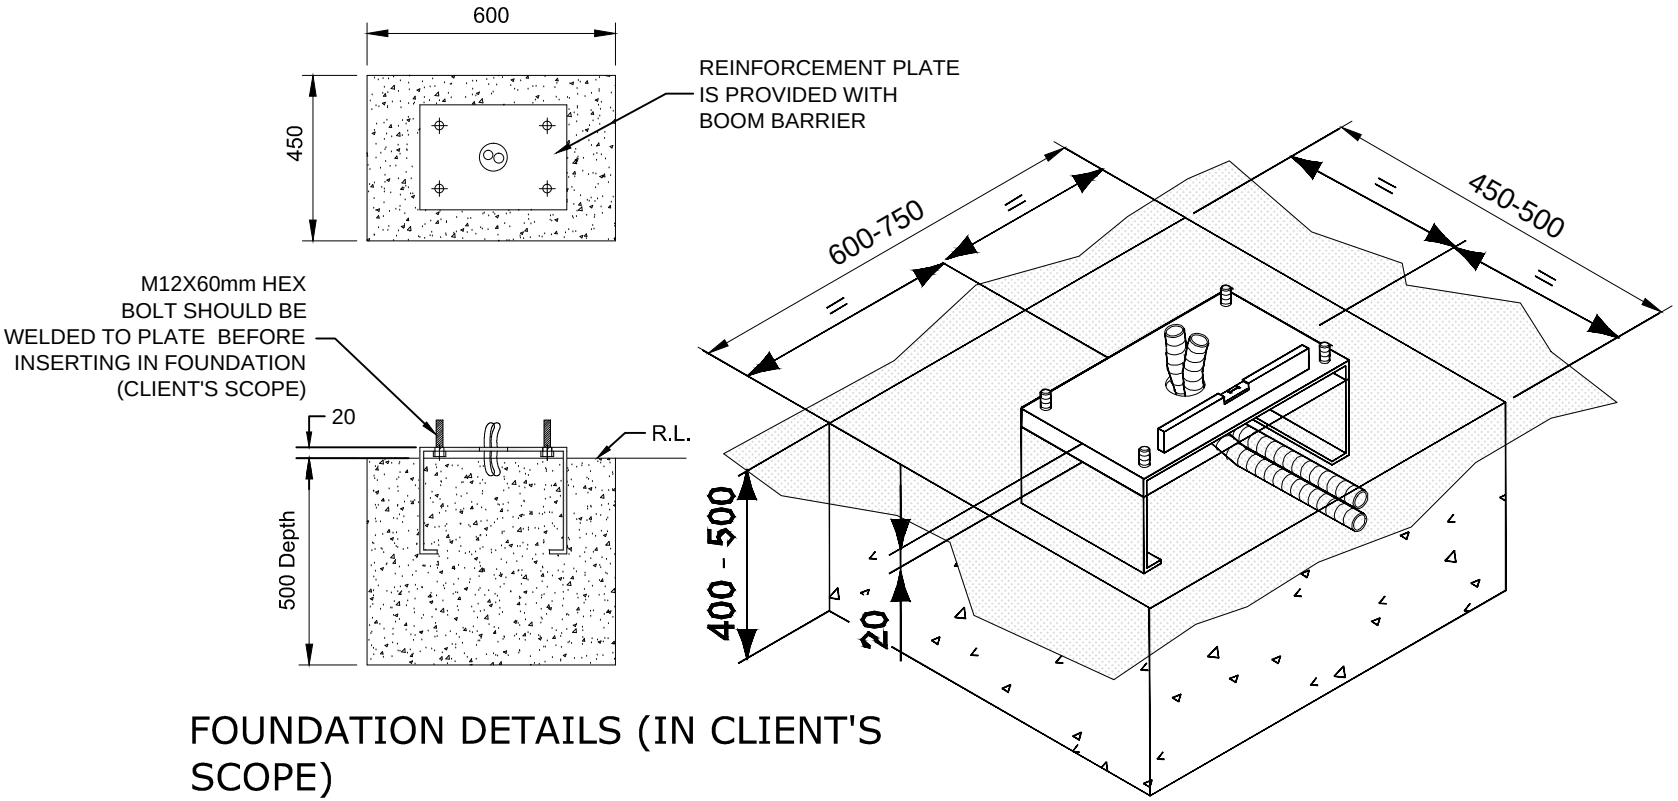


FOUNDATION DETAILS (IN CLIENT'S SCOPE)

NOTE-
1. Reinforcement Details- Reinforcement /foundation plate is provided with boom barrier.
2. Foundation level is same as road level & Reinforcement plate will be 20mm above Foundation Block.
3. Location of Block shown in layout no-TPL-3452-X9790-EC-RC-6118_R0

REV NO	DATE	DESCRIPTION
REV -0	25/11/17	INITIAL DRAWING
REV -1	23/01/18	NOTE IS ADDED

TOLERANCE - ±10mm

This drawing & design is the property of NIHVA TECHNOLOGIES. Not to be sold or copied to any other concern.

TITLE	FOUNDATION FOR BOOM BARRIER		
	SIGN	DATE	
DRAWN	OMKAR	17-11-2017	CLIENT - TATA PROJECTS LIMITED
CHECK	SHEKHAR.	17-11-2017	PROJECT - ALSTOM
APPROVAL	SHEKHAR	17-11-2017	SITE LOCATION - MIHAN,NAGPUR
			DWG. NO. : NIHVA/17-18/0294 REV-0
If any queries contact : projects@nihva.com			SCALE: NTS WT: SHEET: 01 OF 01
ALL DIMENSION ARE IN mm			

NIHVA TECHNOLOGIES PVT. LTD. PUNE
Tel : 020 66304033
Email:- info@nihva.com
Website:- www.nihva.com