Revision		Date	By
A	New measurements, doors redrawn	2022-10-10	EB

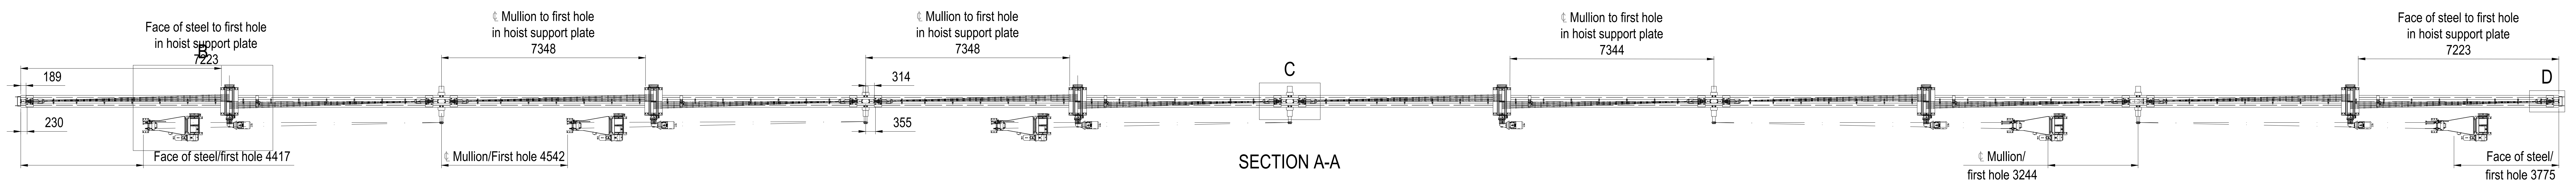

SECTION A-A

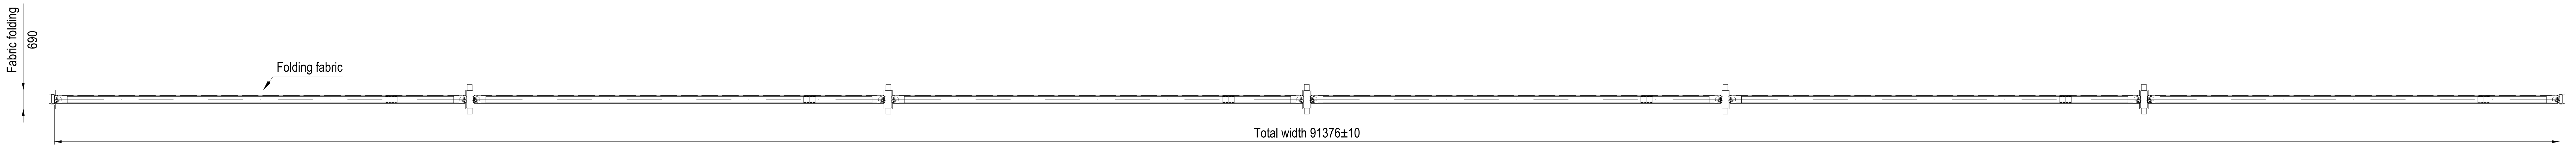

SECTION B-B

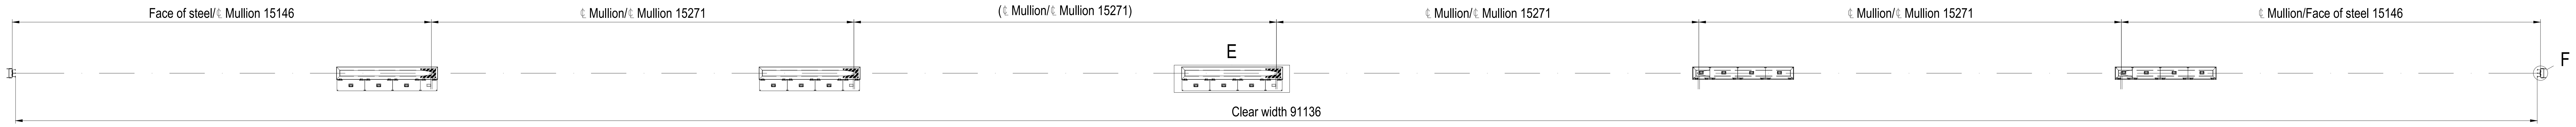
Face of steel/℄ Mullion 15146
℄ Mullion/℄ Mullion 15271
(℄ Mullion/℄ Mullion 15271)
℄ Mullion/℄ Mullion 15271
℄ Mullion/℄ Mullion 15271
℄ Mullion/Face of steel 15146
E
F
Clear width 91136

SECTION C-C

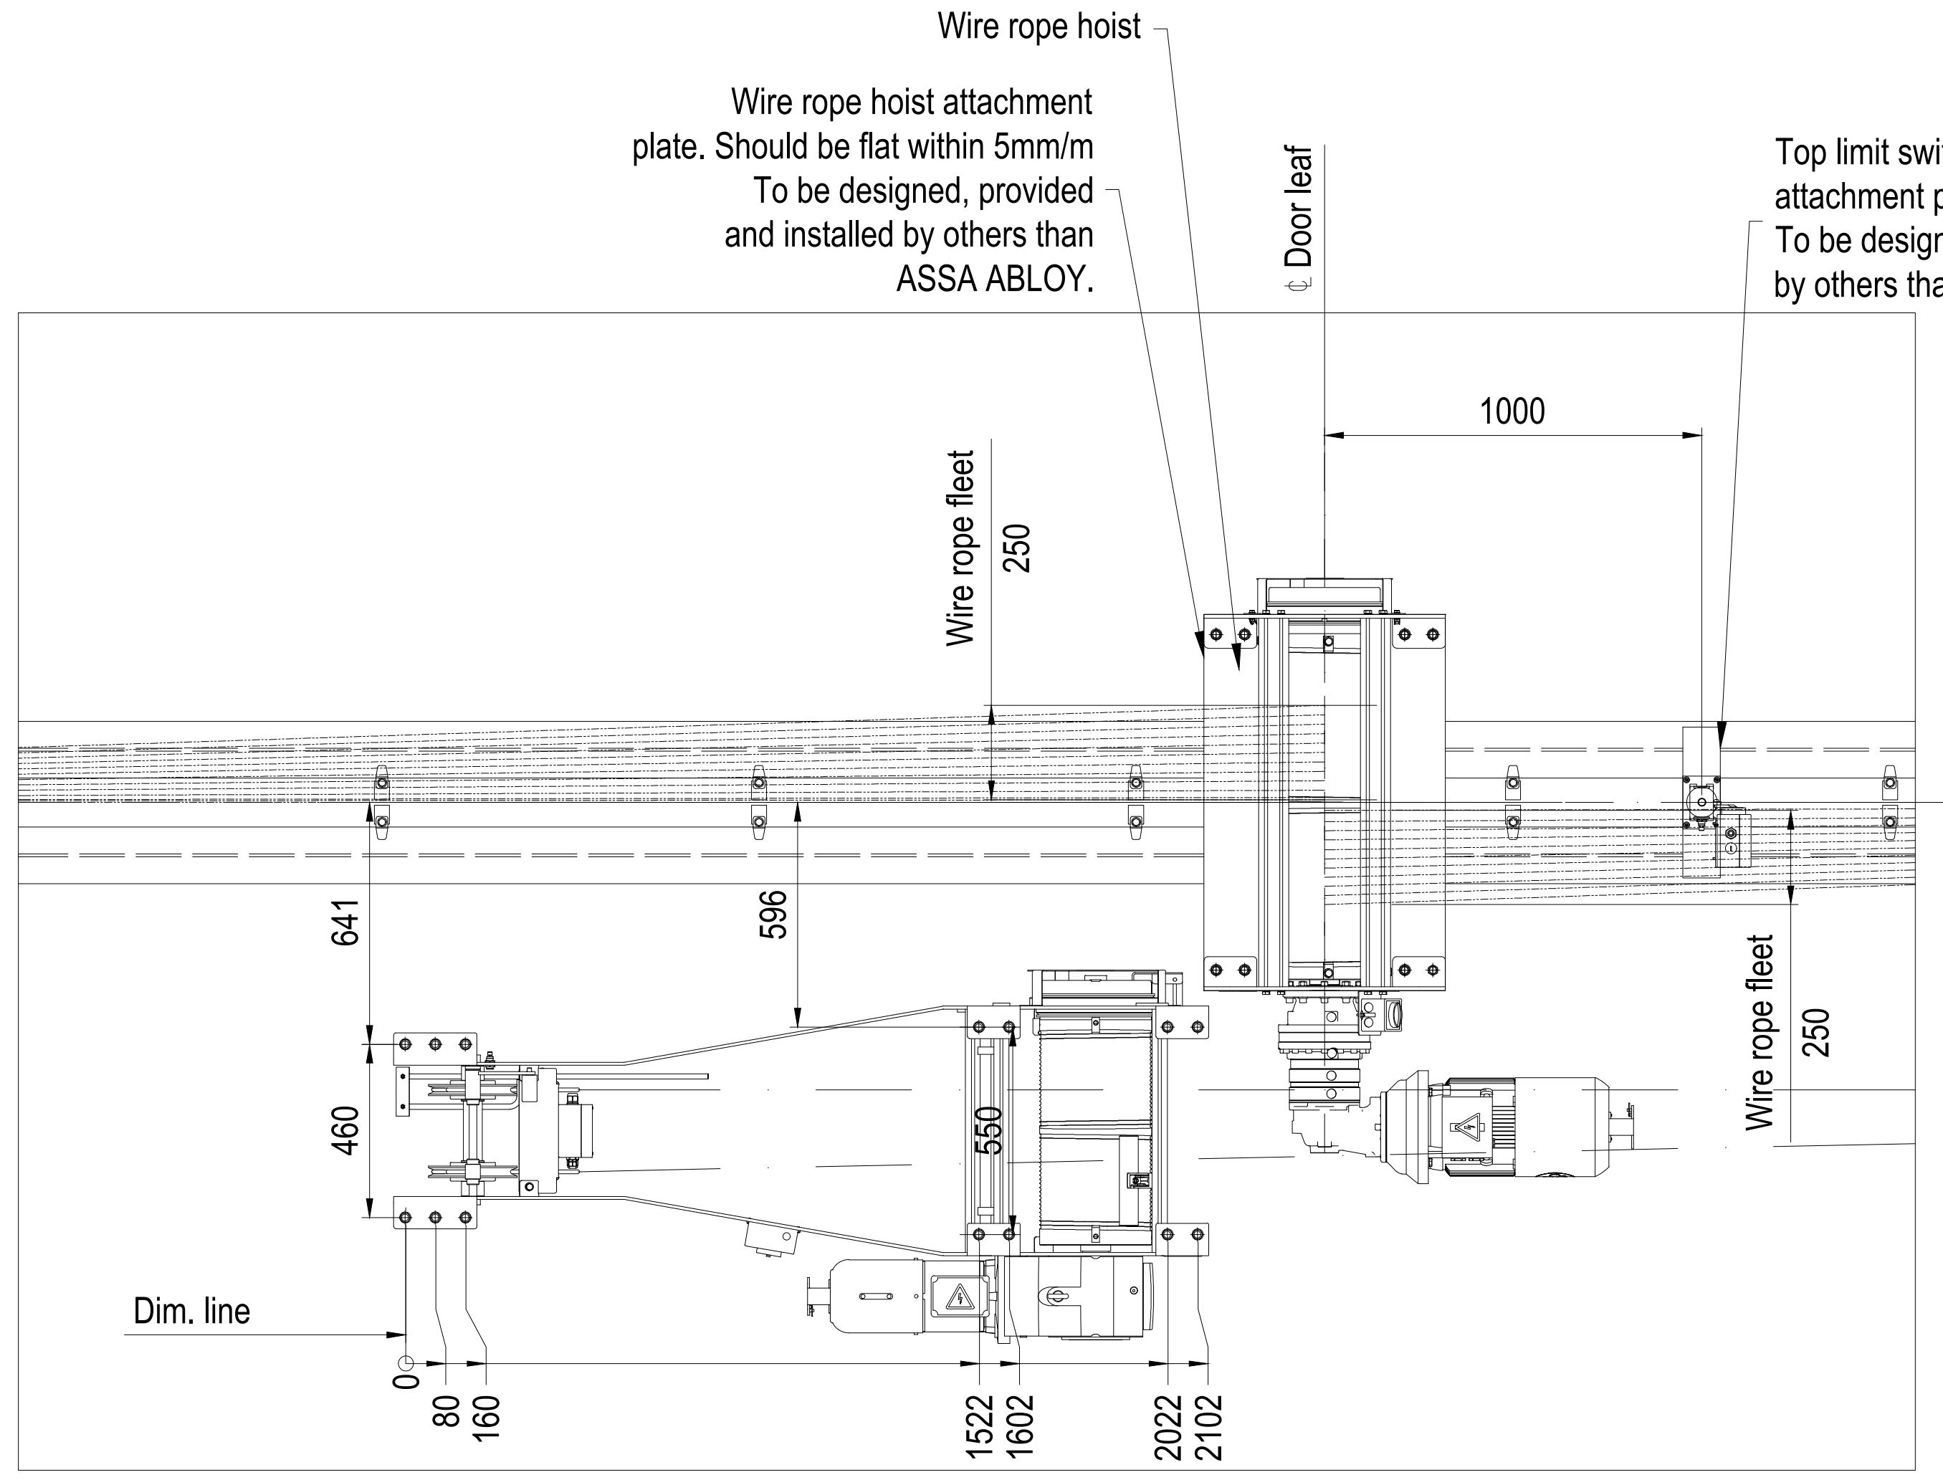

DETAIL B, SCALE (1:20)

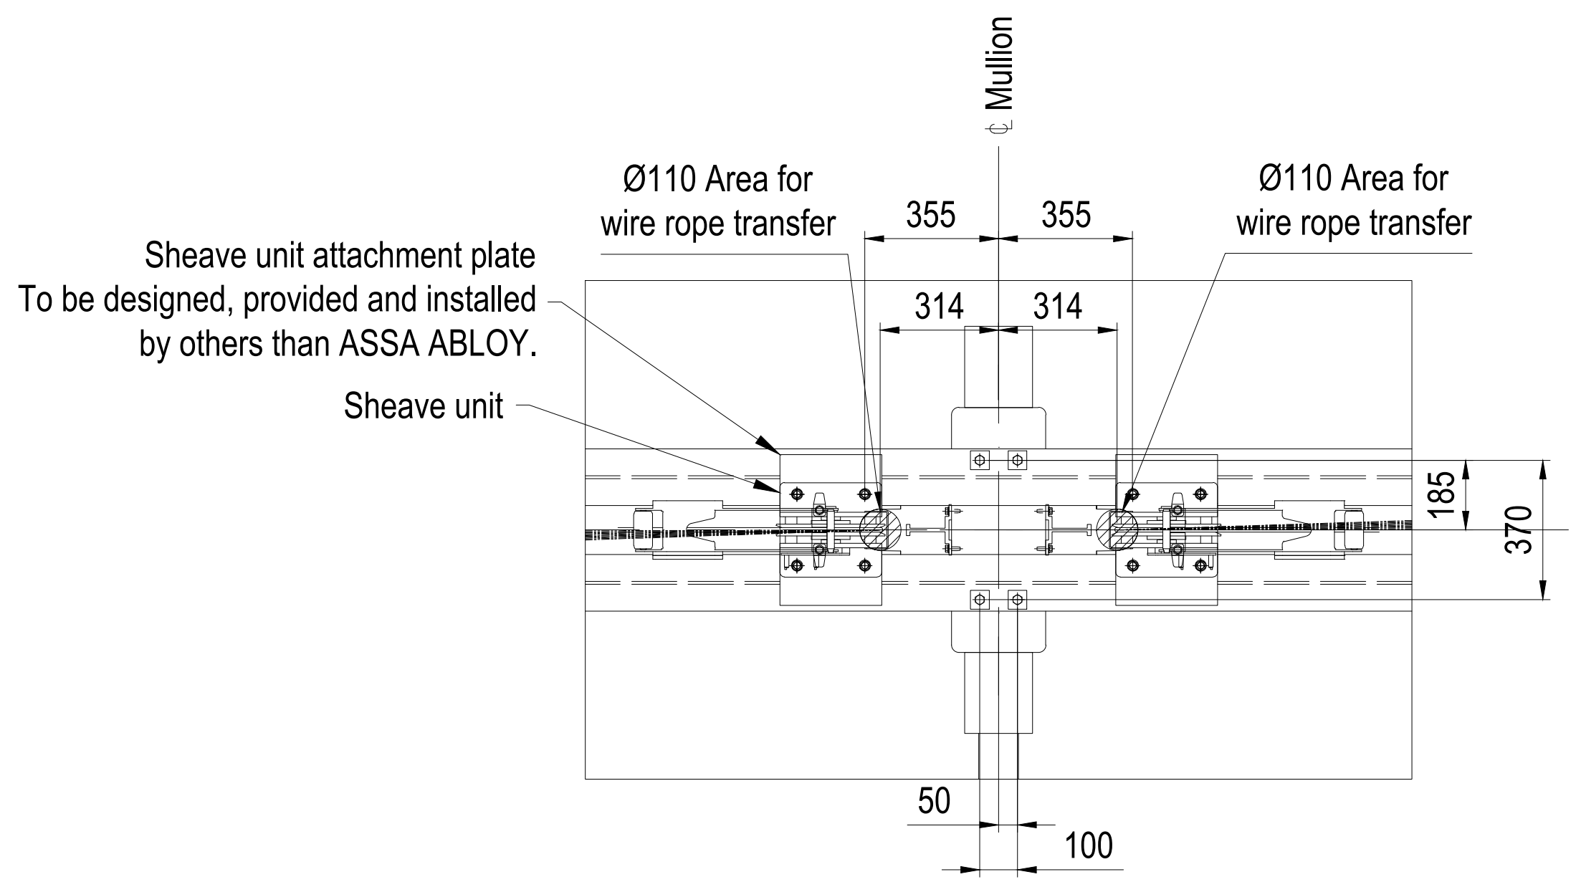

DETAIL C, SCALE (1:20)

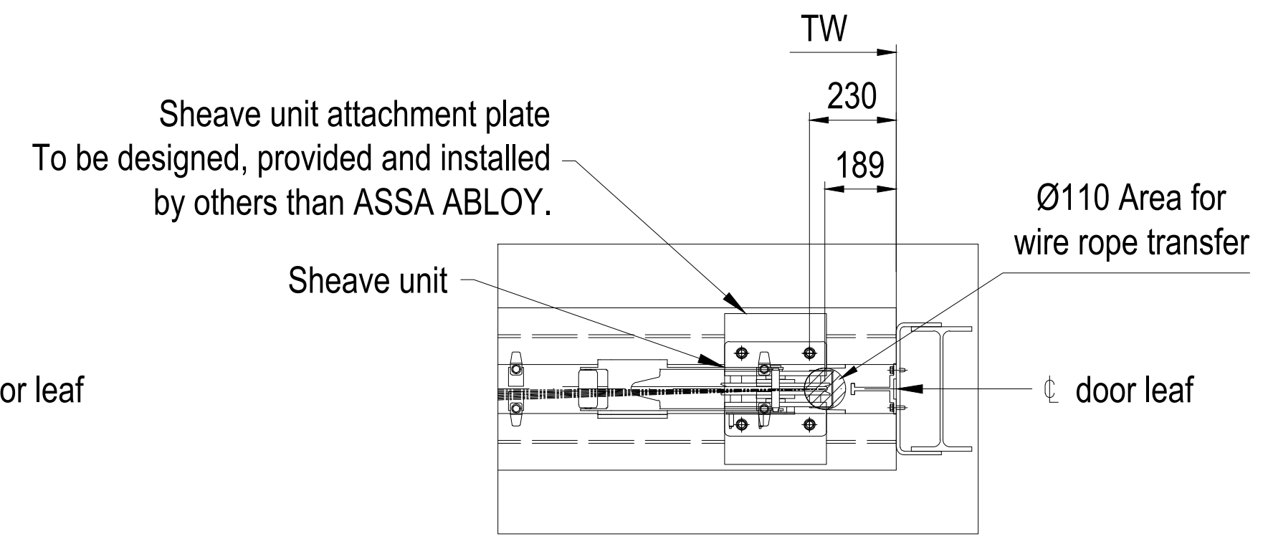
TW
230
189
Sheave unit attachment plate
To be designed, provided and installed
by others than ASSA ABLOY.
Ø110 Area for
wire rope transfer
Sheave unit
℄ door leaf

DETAIL D, SCALE (1:20)

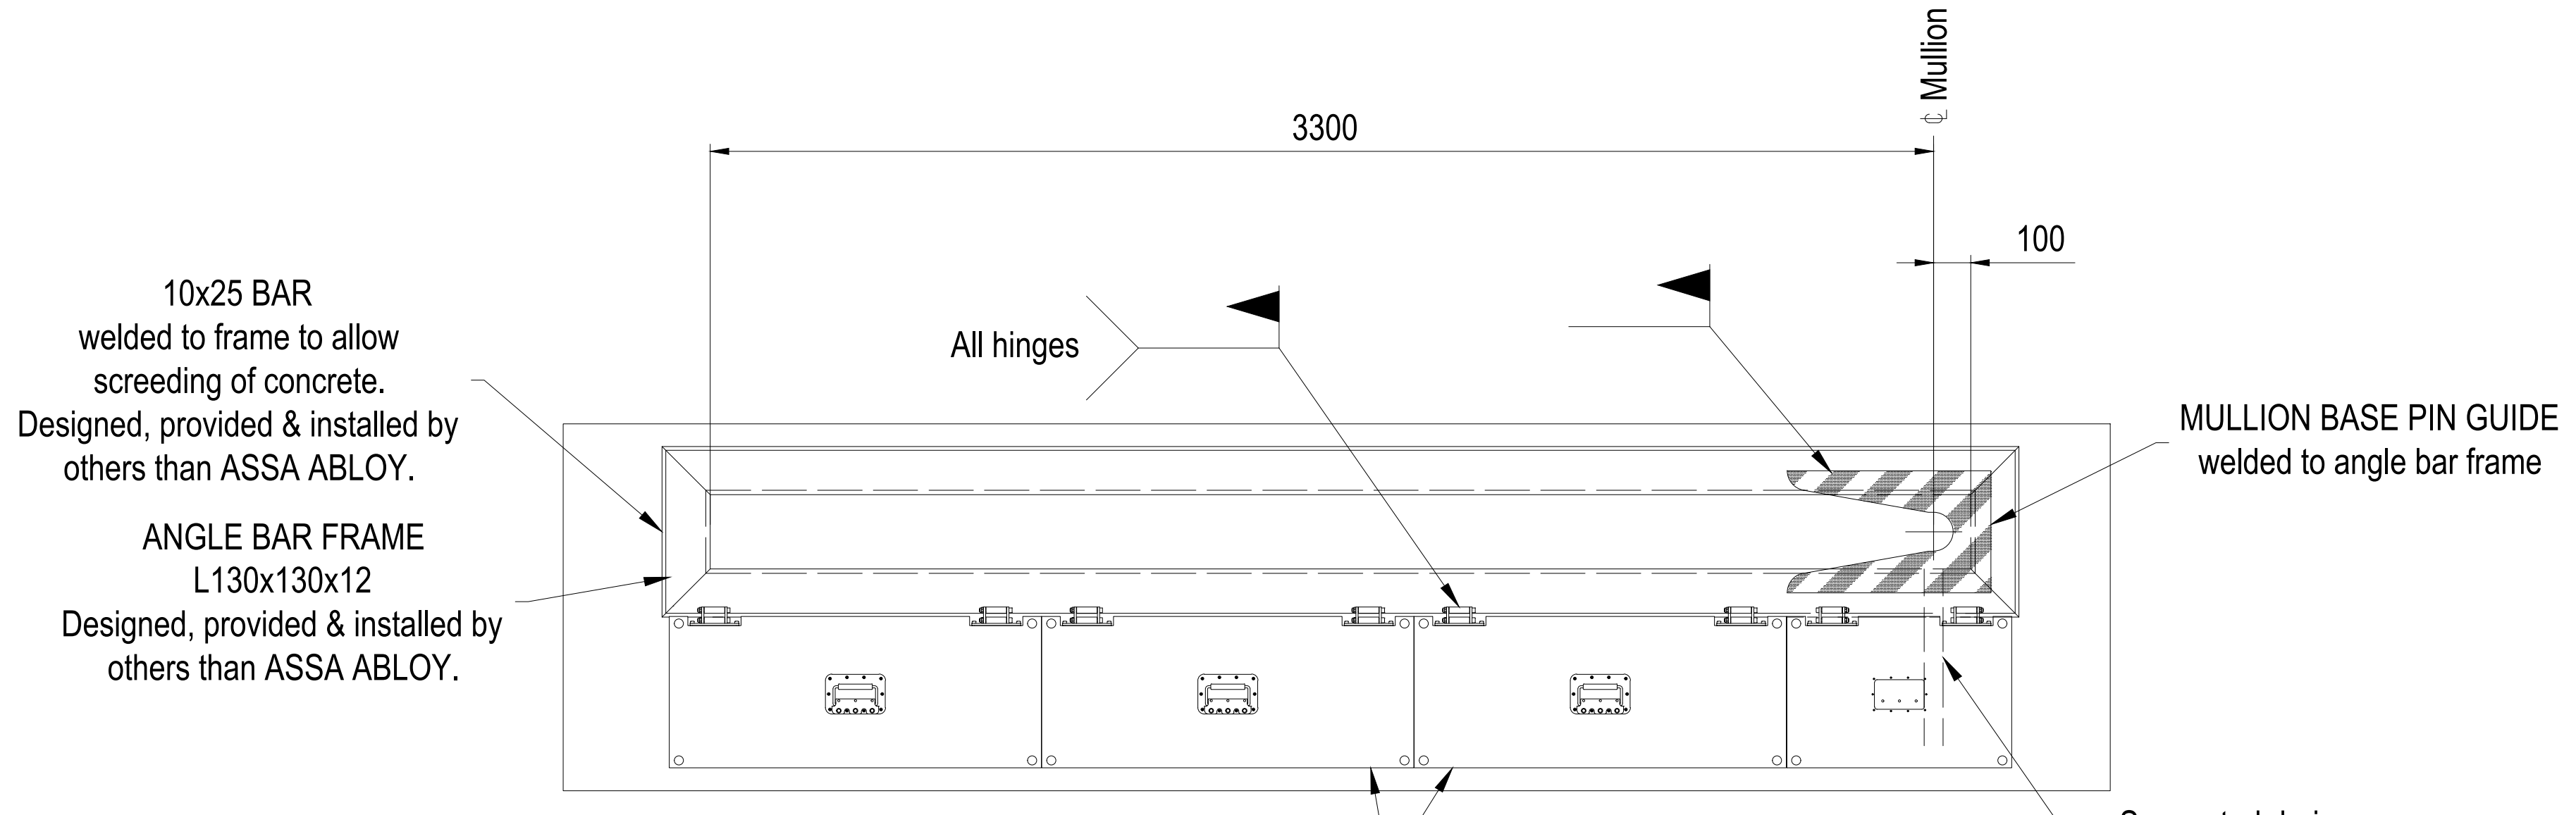

DETAIL E, SCALE (1:20)

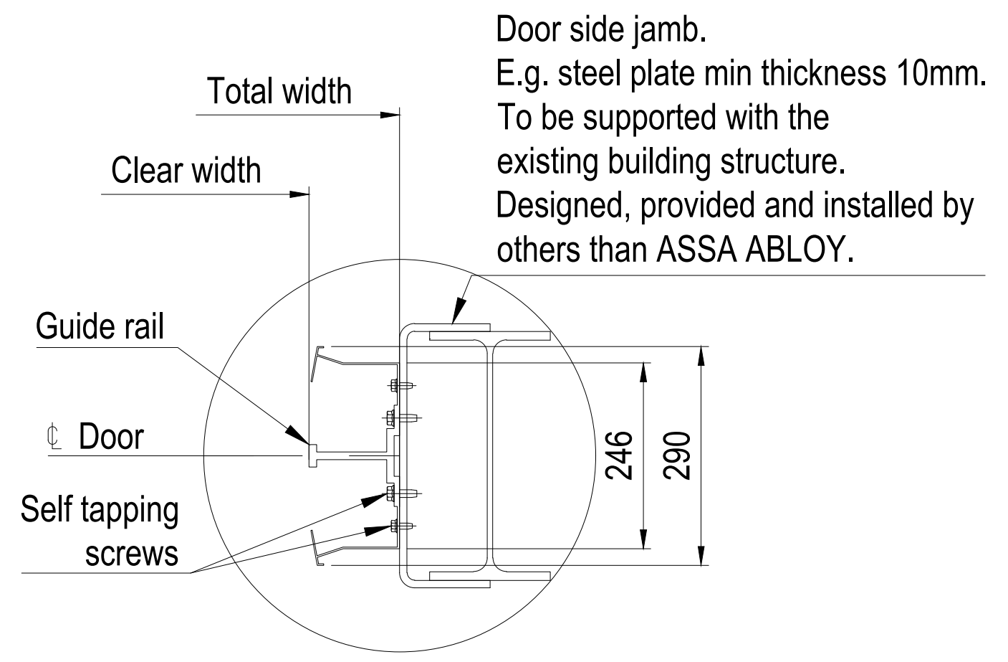

DETAIL F, SCALE (1:10)

DOOR IDENTITY NUMBER: 84801001

LOAD DIAGRAM & NOTES, ref. to drwng. no. 77450

INTERFACE, SECTIONS ref. to drwng. no. 77449

INTERFACE, ELEVATION ref. to drwng. no. 77447

DESIGNED
EB
SIZE A1F
SCALE 1:100
CODE
84801
ITEM NO
DATE
2022-08-30
ASSA ABLOY

If not otherwise stated:
Tolerances
ISO 2768-m
EN ISO 13920-B
Cutting class
ISO 9013-442
Weld class
ISO 5817-C
Surface finish
Smooth raw surface

GMR Aero Technic Hangar2
India
Megadoor 91136x14700/14000
Interface, Plan views

PLOT DATE
DRAWING NO
77448
REVISION
A

This document is the property of ASSA ABLOY Entrance Systems AB and shall not without our written permission be copied, imparted to a third party or used for any other unauthorized purpose.