


Abbrevation's:
WOW-Wall Opening Width
WOH-Wall Opening Height
UC-Under Cut
FFL-Finished Floor Level

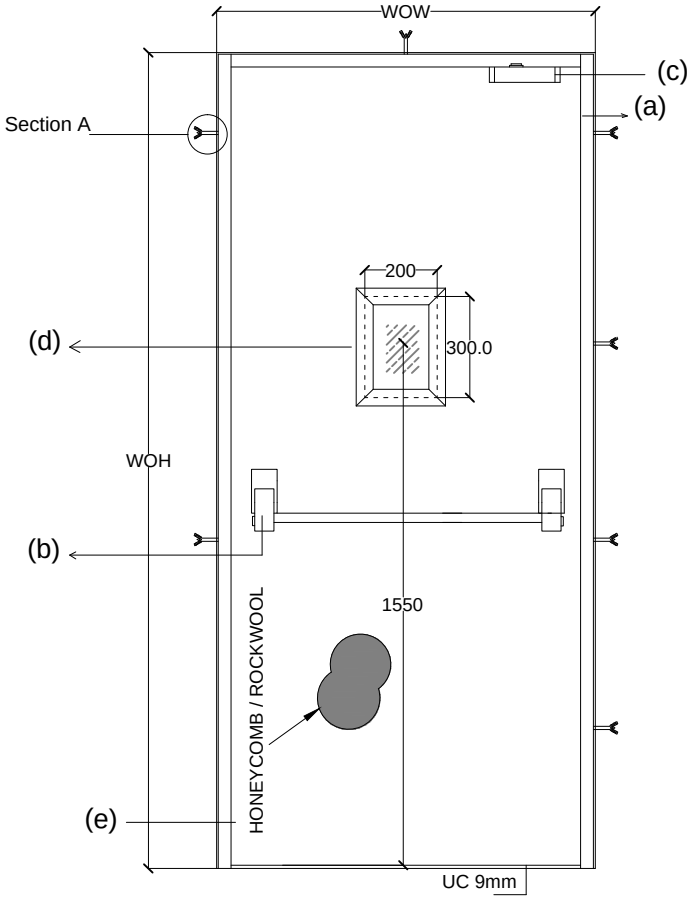

Inside Elevation

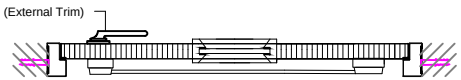

Top View

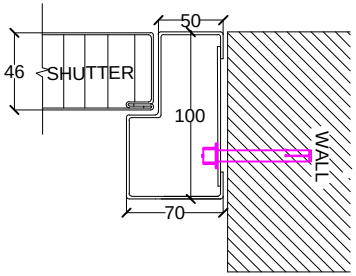

Detail view of Section A

ASSESORIES DETALES

(a) HINGES: SS Ball bearing butt hinges 100x75x3mm

(b) LOCK : Panic bar with external trim


(c) DOOR CLOSER: DORMA TS68

(d) GLASS : Vision Glass of size 200x300mm

(e) CONCEALED FLUSH BOLT

Shutter thickness : 46 mm
Frame Sheet thick : 1.5mm
Shutter sheet thick : 1.2mm
Fixing : On Solid Brick plasterd wall with Anchors

NOTE:- *All Dimensions are in mm.
*Tolerance:-All Linear Dimensions ±3mm,Others ±0.5mm.
*The Drawing Is For Location of Hardware only. Drawing Does Not Represent The Hardware For More Clarity, Please Go Through Hardware Broucher.

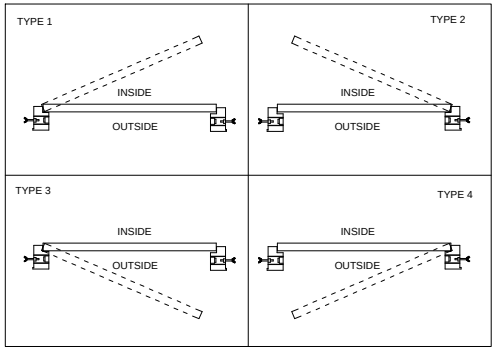

COLOR
1.TRAFFIC WHITE (RAL 9016)
2.LIGHT GREY (RAL 7035)
3.GENTION BLUE (RAL 5010)
4.SIGNAL RED (RAL 3001)

FIRE RATED EXIT DOOR							
SR. NO.	WOW	WOH	TYPE 1	TYPE 2	TYPE 3	TYPE 4	QUANTITY
01	1200mm	2400mm			6	3	9

DIMENSION :

CLEAR WIDTH	CLEAR HEIGHT	QUANTITY
1200mm	2400mm	09 NOS

MATERIAL :

THICKNESS :

NOTE:-
1.CLIENT SHOULD MENTION COLOR FOR DOOR.
2.CLIENT SHOULD CHECK DOOR ORIENTATION & APPROVE THE SAME.

REV NO	DATE	DESCRIPTION
REV 1	07-11-2017	QTY OF DOOR INCREASED

NIHVA TECHNOLOGIES PVT. LTD. PUNE
Email:- info@nihva.com
Website:- www.nihva.com

TITLE:

FIRE RATED EXIT DOOR

CLIENT'S APPROVAL :

CLIENT - ASHOK CONSTRUCTIONS

PROJECT - DSM

SITE LOCATION - RANJANGAON

DWG. NO. : NIHVA/15-16/0261/R01 REV. - 1

SCALE: NTS WT: SHEET:1 OF 1

NAME	SIGN	DATE
DRAWN : SURAJ		07-11-2017
CHECK : OMKAR		04-11-2017
APPD : SHEKHAR.		04-11-2017

If any queries contact : projects@nihva.com

NOTE: ALL DIMENSIONS ARE IN mm

THIS DRAWING & DESIGNING IS THE PROPERTY OF NIHVA TECHNOLOGIES. NOT TO BE SOLD OR COPIED TO ANY OTHER CONCERN.