


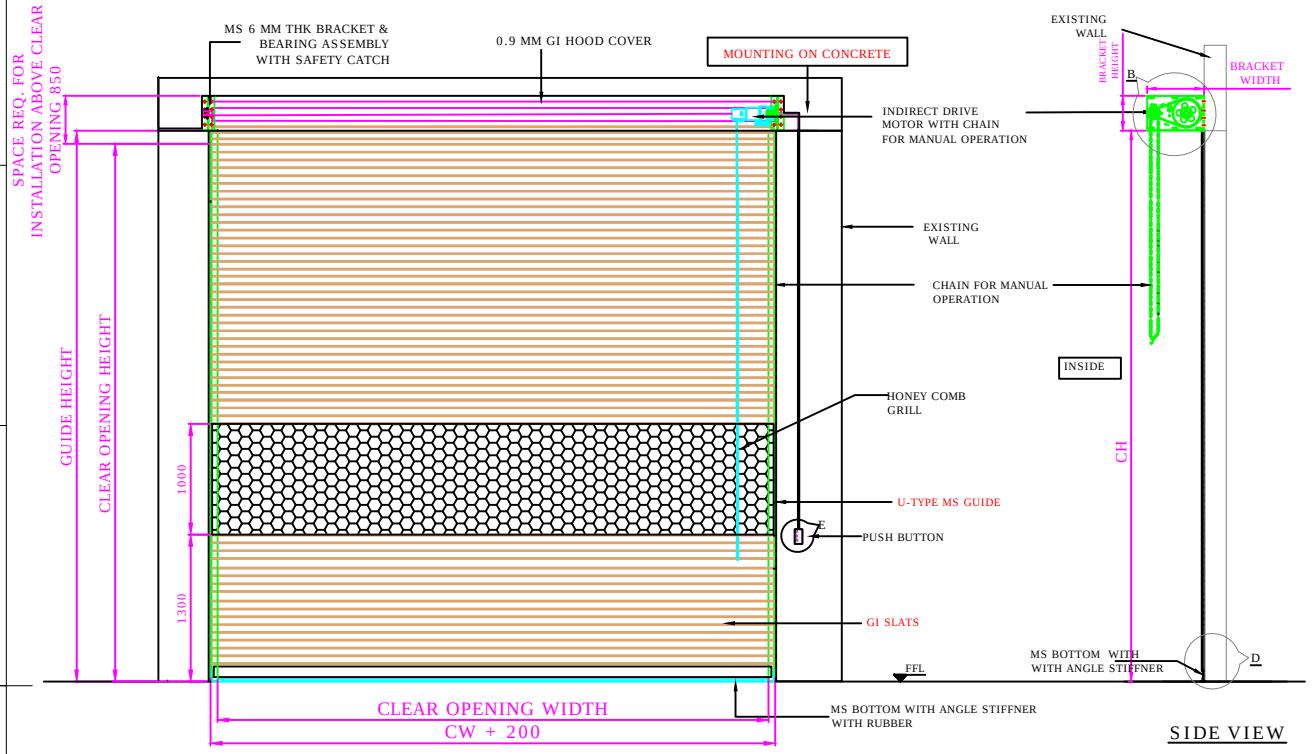


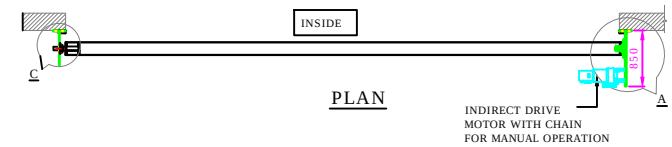


PLAN

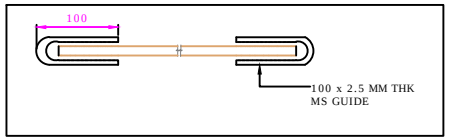


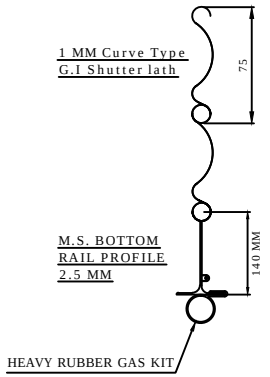


DETAILS : D

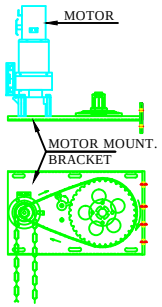

DETAILS : A & B

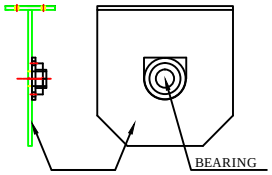

DETAILS : C

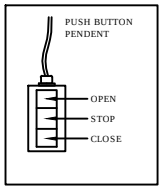

DETAILS : E

RAL CODE	SHADE	COLOUR
RAL 9006	WHITE ALUMINIUM	

SR NO	CLEAR WIDTH(CW)	CLEAR HEIGHT(CH)	QTY	LOCATION	MOTOR SIDE (RH/LH)
4	2500	3000	2		
3	5300	4000	1		
2	4650	4000	1		
1	3950	3200	2		

NOTES-
(1) IF REQUIRED M.S. STRUCTURE , FITTING & ALL CIVIL WORK IN CLIENT SCOPE .
(2) KINDLY CONFIRM INSTALLATION LOCATION & MOTOR SIDE AS SEEN FROM INSIDE(RH=STANDARD) .

This drawing & design is the property of NIHVA TECHNOLOGIES. Not to be sold or copied to any other concern.

TITLE- GI SLAT MOTORIZED ROLLING SHUTTER

NIHVA TECHNOLOGIES PVT. LTD.

NIHVA TECHNOLOGIES PVT. LTD. PUNE
Tel : 020 66304033
Email:- info@nihva.com
Website:- www.nihva.com

	NAME	SIGN	DATE
DRAWN	SIDDHESHWAR		28.12.2020
CHECK	A.K.		28.12.2020
APPRD.			

CLIENT - LUPIN LIMITED
PROJECT - LUPIN LIMITED
SITE LOCATION - PUNE
If any queries contact : projectsupport@nihva.com
DWG. NO. : NIHVA/20-21/0116 REV- R00
ALL DIMENSION ARE IN mm
SCALE: NTS WT: SHEET: