



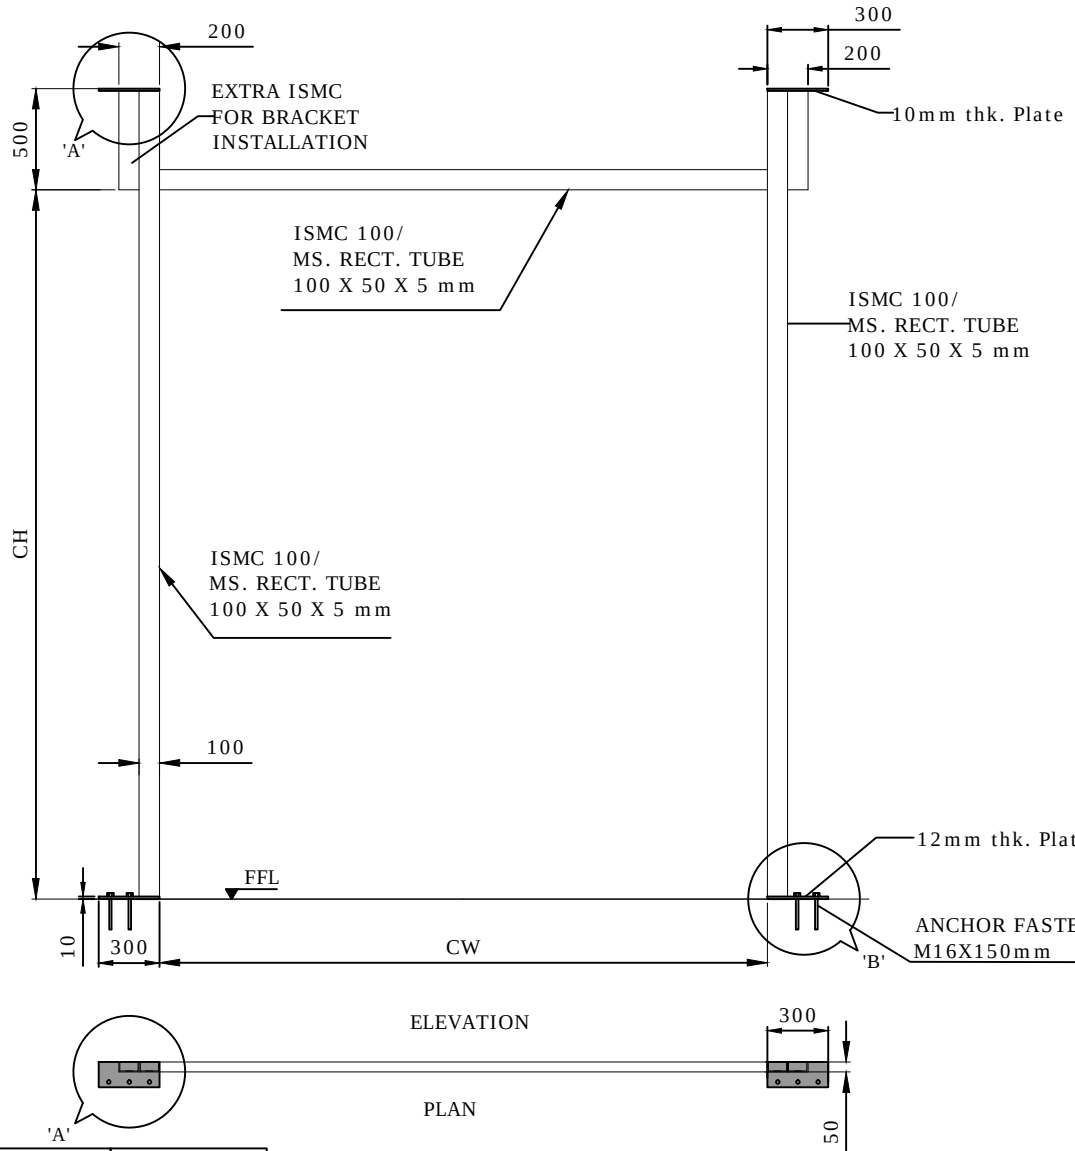


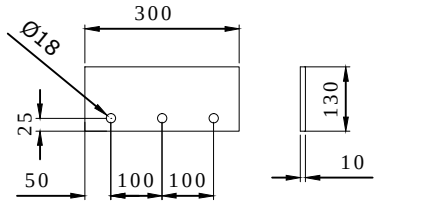

DETAIL VIEW 'A'
UP SIDE PLATE

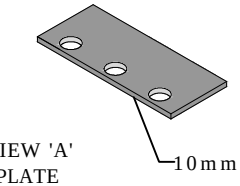

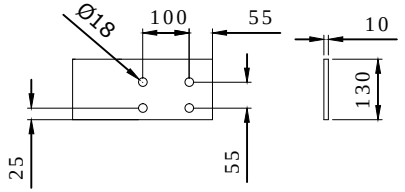

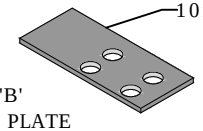

DETAIL VIEW 'B'
BOTTOM SIDE PLATE

CLEAR WIDTH (CW)	CLEAR HEIGHT (CH)	QUANTITY
3000	3000	1
4000	4000	1

REV:-01).07-06-2018
STRUCTURE BOTTOM AND UP SIDE ADDED PLATE (130X300mm)

This drawing & designing is the property of NIHVA TECHNOLOGIES. Not to be sold or copied to any other concern.

TITLE
STRUCTURE DETAILS FOR ROLLING SHUTTER

	NAME	SIGN	DATE
DRAWN	SURAJ		02.06.18
CHECK	PRADEEP		02.06.18
APPROVAL	PRADEEP		02.06.18
MFG.			

If any queries contact : design@nihva.com

ALL DIMENSION ARE IN mm

NIHVA TECHNOLOGIES PVT. LTD.
NIHVA TECHNOLOGIES PVT. LTD. PUNE
Tel : 020 66304033
Email:- info@nihva.com
Website:- www.nihva.com

CLIENT - Shapoorji Pallonji and Co.Pvt Ltd
PROJECT -
SITE -
DWG. NO. : NIHVA/18-19/0052/R01 | REV-01
SCALE: NTS | WT: | SHEET: 01 OF 01