
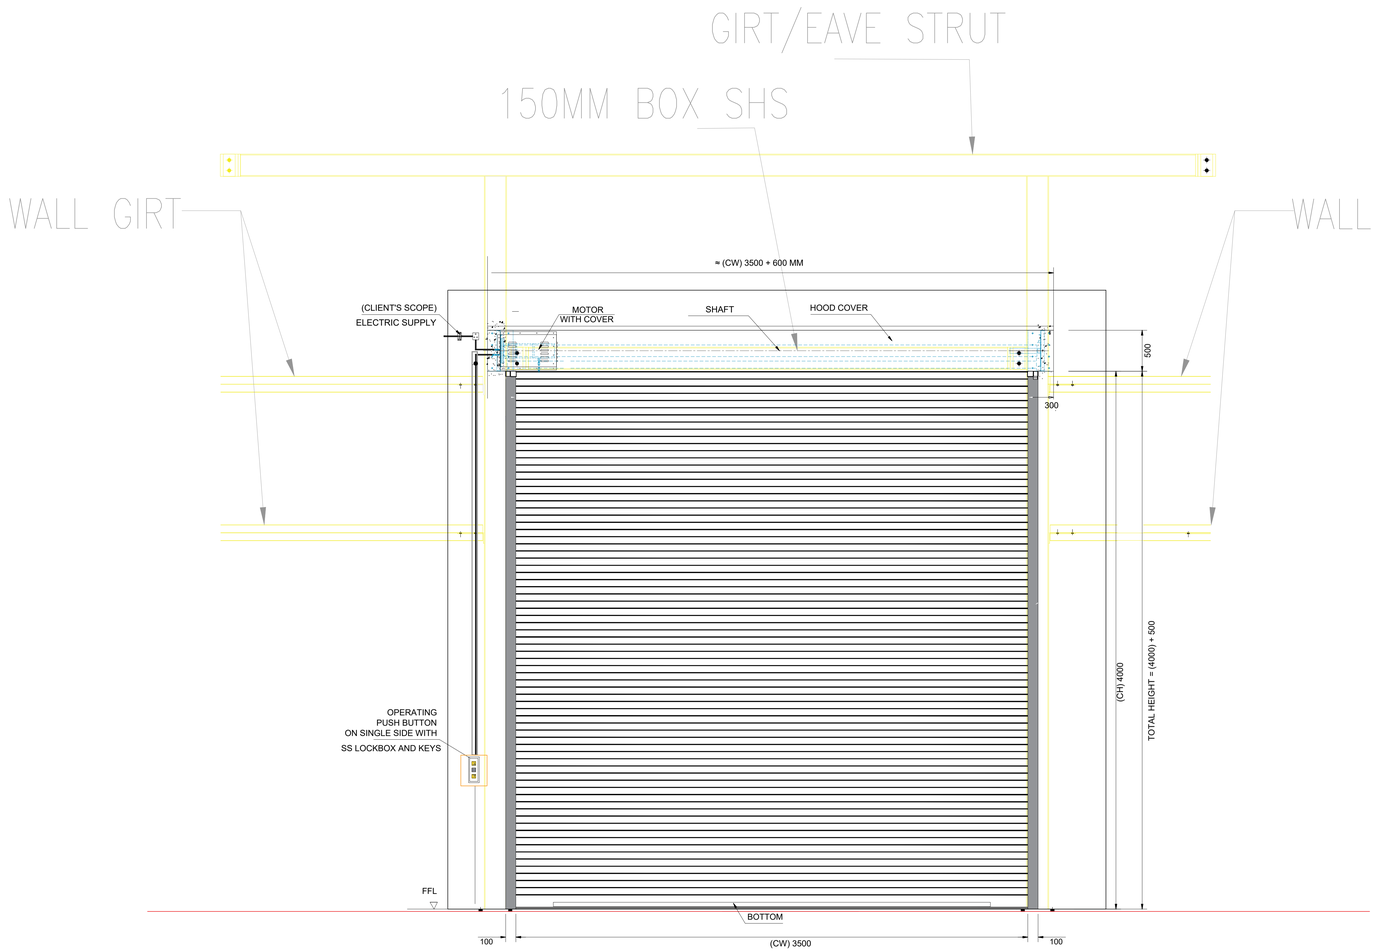
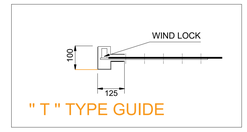



INSIDE ELEVATION

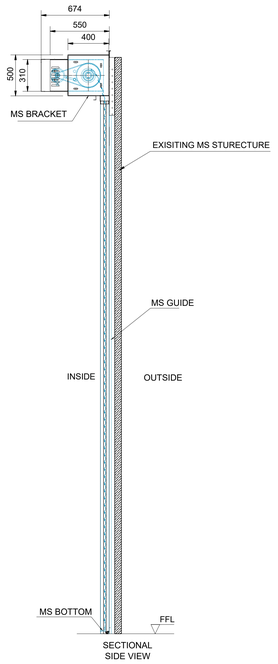


## TECHNICAL SPECIFICATION:-

| SR. | SPECIFICATION | DETAILS |
|---|---|---|
| 1. | Description & Drive | Motorized Rolling Shutter ( Direct Drive With CE Certificated ) |
| 2. | Location Area | Inside |
| 3. | Mounting Surface | MS STRACTURE |
| 4. | Slat | AS PER NIHVA STD. |
| 5. | Bottom Profile | MS Plate 100 x 2.5 mm thick with Angle Stiffner with rubber seal |
| 6. | Guide Profile | M.S." T " Shape profile 100 x 3 mm Thk. |
| 7. | Hood Cover & Motor Cover | Made of GI Sheet Thickness 0.9 mm |
| 8. | Surface finish | SYNTHETIC ENAMEL PAINT RAL SHADE 9002 |
| 9 | Accessories | Push Button Single side |

## SHUTTER SIZES :-

| SR. | CLEAR WIDTH | CLEAR HEIGHT | QTY. |
|---|---|---|---|
| 01 | 3500 mm | 4000 mm | 3 |

Note :-

1. All Dimension are in mm
2. This drawing is only for understanding purpose

This drawing & designing is the property of NIHVA TECHNOLOGIES. Not to be sold or copied to any other concern.

TITLE :- MOTORISED ROLLING SHUTTER

NIHVA TECHNOLOGIES PVT. LTD. PUNE
Tel : 020 66304033
Email:- info@nihva.com
Website:- www.nihva.com

| | NAME | DATE |
|---|---|---|
| DRAWN | B.S. | 13/02/2025 |
| CHECK | V.M. | 13/02/2025 |
| APPROVAL | V.T. | 13/02/2025 |

CLIENT - SMP INFRASTRUCTURE PVT. LTD.
PROJECT - ROLLING SHUTTER
FORMAT NO - NIHVA-DD-F-03
DWG. NO. : NIHVA/24-25/SMP/250124 REV-02
SCALE: NTS WT: SHEET: 01 OF 01
ALL DIMENSION ARE IN mm
If any queries contact : design@nihva.com