




Prinzipzeichnung RapidProtect RP300
General drawing Rapid Protect RP300

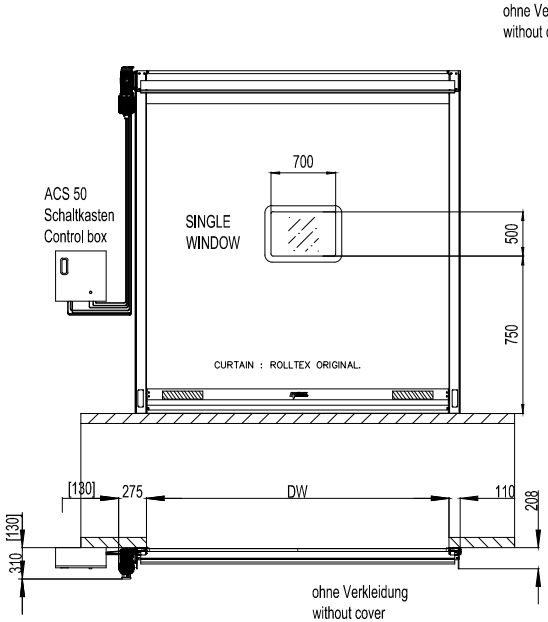


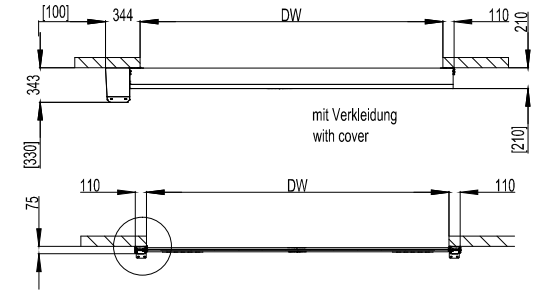

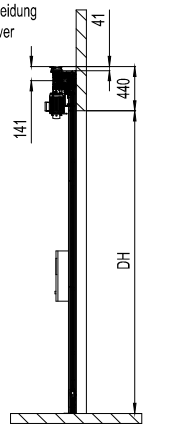

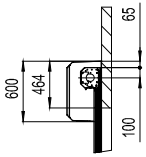

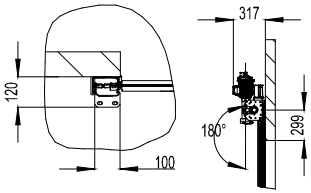

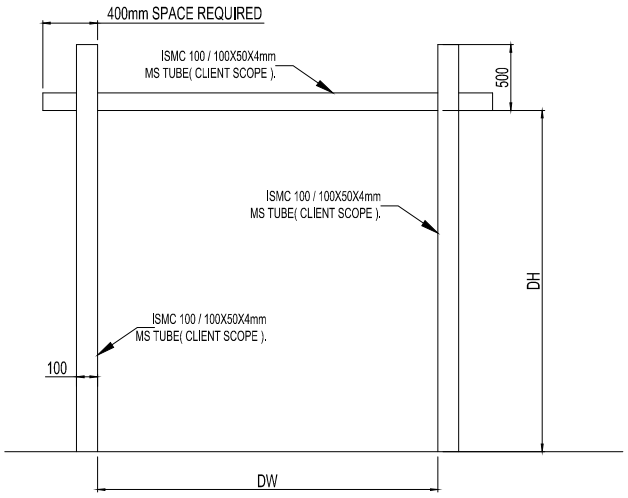

MS STRUCTURE

DOOR SIZE		
DW	DH	QUANTITY
1500	2000	8

RAL 1003	
RAL 2004	
RAL 3000	
RAL 5002	
RAL 6005	
RAL 7035	
RAL 9005	
RAL 9010	

Toleranz ±3 mm (gültig für alle Maßangaben) Tolerance ±3 mm (for all dimensions)
Maßangaben in [ ] ==> Montagefreiraum Dimensions in [ ] ==> clearance for installation

NOTE-
1. COLOR : RAL 5002 (BLUE).
2. CURTAIN : ROLLTEX ORIGINAL.
3. REQUIRED STRUCTURE FOR HSD WILL BE IN CLIENT'S SCOPE.

REV.NO	DESCRIPTION	DRAWN	DATE	SIGN
R01	2.WINDOW SIZE CHANGED. 1.ADDED RAL COLOUR	SURAJ	22-10-2018	

This drawing & designing is the property of NIHVA TECHNOLOGIES. Not be sold or copy to any other concern.

TITLE: HIGH SPEED DOOR RP 300 & STRUCTURE

	NAME	SIGN	DATE
DRAWN	P.A		21.10.2018
CHECK	R.D		21.10.2018
REV.	V.T		21.10.2018
APPROVAL			

If any queries contact : sales@nihva.com

ALL DIMENSIONS ARE IN mm

NIHVA
NIHVA TECHNOLOGIES PVT. LTD.
Website:- www.nihva.com
NIHVA TECHNOLOGIES PVT. LTD. PUNE
Tel : 020 66304033
Email:- info@nihva.com

CLIENT - FINEARC SYSTEMS LTD
PROJECT -
SITE - PUNE
DWG. NO. : NIHVA/18-19/0156/R01 REV:- 01
SCALE: NTS WT: SHEET: 01 OF 01