
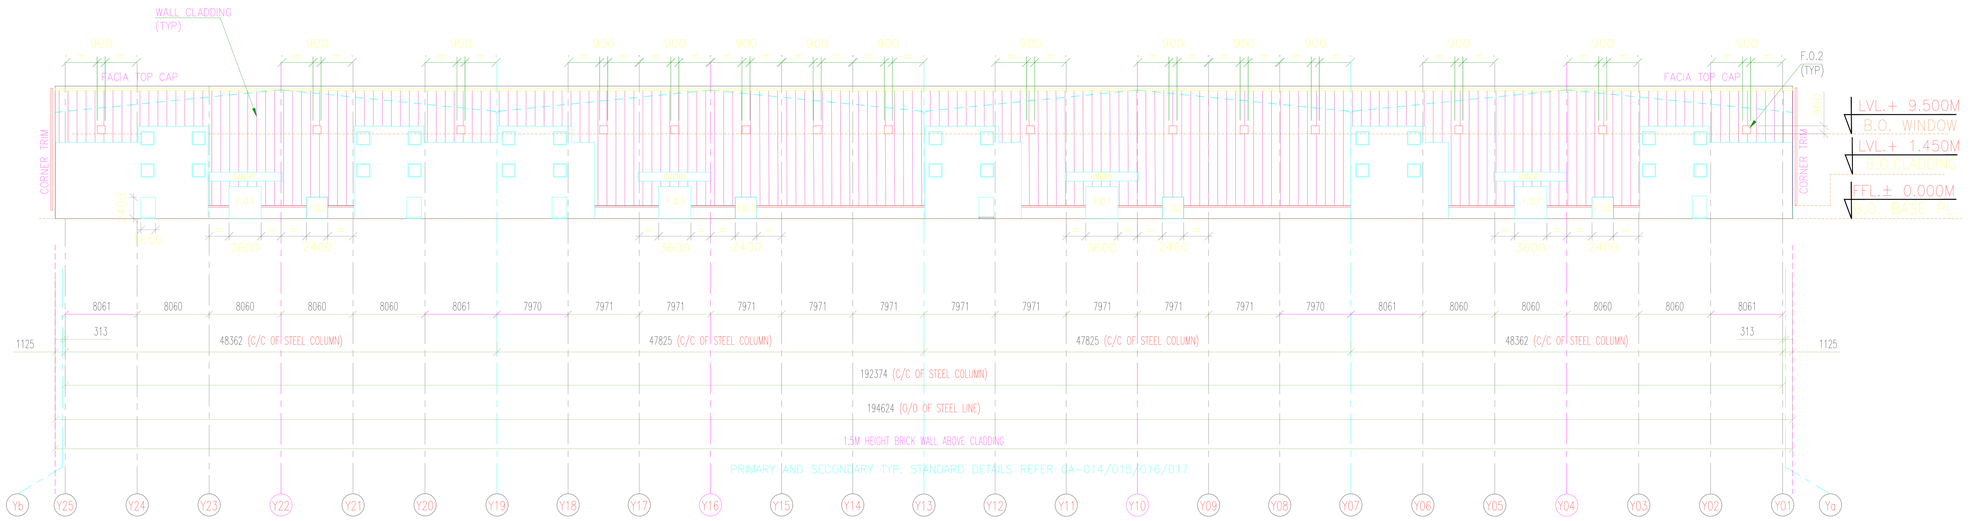


END WALL SHEETING ELEVATION ALONG GRID-X01

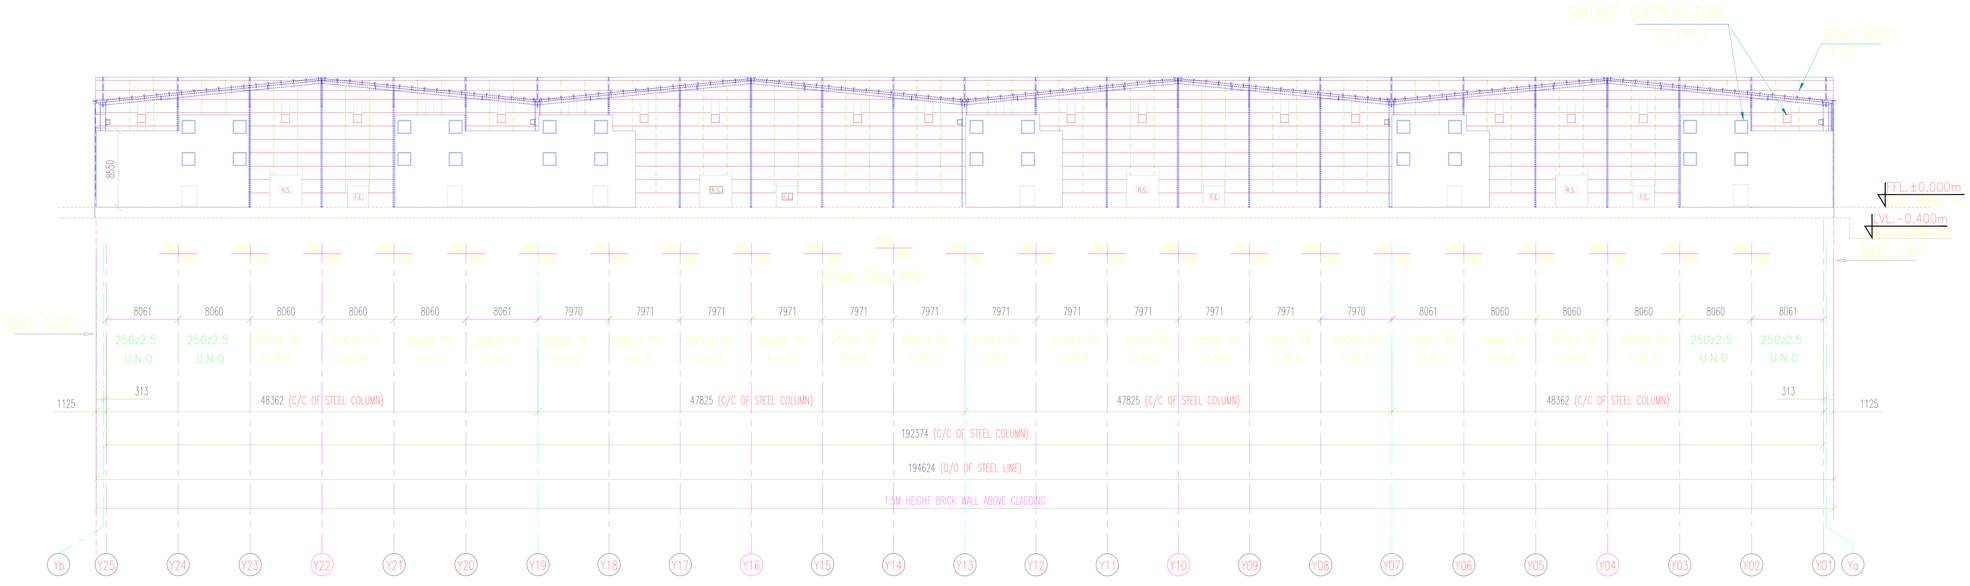

END WALL FRAMING ELEVATION ALONG GRID-X01

▽ DENOTES FOR ISA 50X50X3 W/M12 @ EACH END & 5 Thk. GUSSET
ALL SAG ROD 12 DIA (U.N.O)
ALL JAMB & HEADER 250c2.0 (U.N.O)
PRIMARY AND SECONDARY TYP. STANDARD DETAILS REFER GA-014/015/016/017

SCHEDULE FOR OPENING

S.No.		WIDTH	HEIGHT	No. OF QTY.
1.	F.0.1	3600	3600	4
2.	F.0.2	2400	2400	4
3.	F.0.3(SMOKE EXTRACTOR)	900	900	16

GOOD FOR RECORDS

ISSUED FOR APPROVAL

SENT ON .....

IN ORDER TO SCHEDULE THIS PROJECT IN THE MOST EFFICIENT MANNER, RETURN THESE DOCUMENTS, MARKED WITH YOUR COMMENTS, WITHIN TWO WEEKS FROM THE ABOVE MENTIONED DATE.
ANY CHANGES MADE AFTER APPROVAL OF THESE DRAWINGS MAY DELAY THE FABRICATION AND DELIVERY PROCESS.
THESE DRAWINGS ARE NOT FOR CONSTRUCTION.

1. ☐ APPROVED
NO CHANGES. PROCEED WITH FABRICATION.
2. ☐ APPROVED AS NOTED
FABRICATION MAY PROCEED ON THE BASIS OF CORRECTIONS INDICATED.
3. ☐ NOT APPROVED, RE-SUBMIT FOR APPROVAL.

REVIEWED BY .....
NAME
SIGNATURE DATE

Rev.	Description	Name	Checked	Date
R2	GOOD FOR RECORDS	P.B./B.R.	A.A./M.S.	26/05/2023
R1	REVISED AS PER CLINT COMMENT	P.B./B.R.	A.A./M.S.	19/05/2023
R0	ISSUED FOR APPROVAL	P.B.	A.A./M.S.	30/03/2023

REVISIONS

Project: Pre Engineering Building At GMR-DELHI INTERNATIONAL AIRPORT LTD., NEW DELHI

Client: GMR-DELHI INTERNATIONAL AIRPORT LTD. NEW DELHI

Process Consultant:

Detailed Engineering Consultant:

Building: GA PARKING

Drawing Title: END WALL FRAMING & SHEETING ELEVATION

Everest Industries Limited
ESBS Division, Level 3, Tower 14, Solitaire Corporate Park, Chakala, Andheri (E), Mumbai-400093, India.
Website : www.everestind.com

Drawn by:	P.B.	Scale: 1:500	Date: 30/03/2023	
Checked by:	A.A./M.S.	Project No: ESBS/PB-02434:01.01.01	Drawing No: GA-011	Revision: R2
Design By	A.A.			

NOTE:-
1. All rights reserved. This drawing contains proprietary information which is protected by copyright. No part of this drawing may be reproduced, translated in computer language, or transmitted in any form whatsoever without the prior written consent of EVEREST INDUSTRIES LIMITED

SHEET SIZE-A3